


**GROUND FLOOR**

# EVACUATION MAP

## GROUND FLOOR DORMITEL

### HALLWAY IN BETWEEN ROOM 103 AND ROOM 104

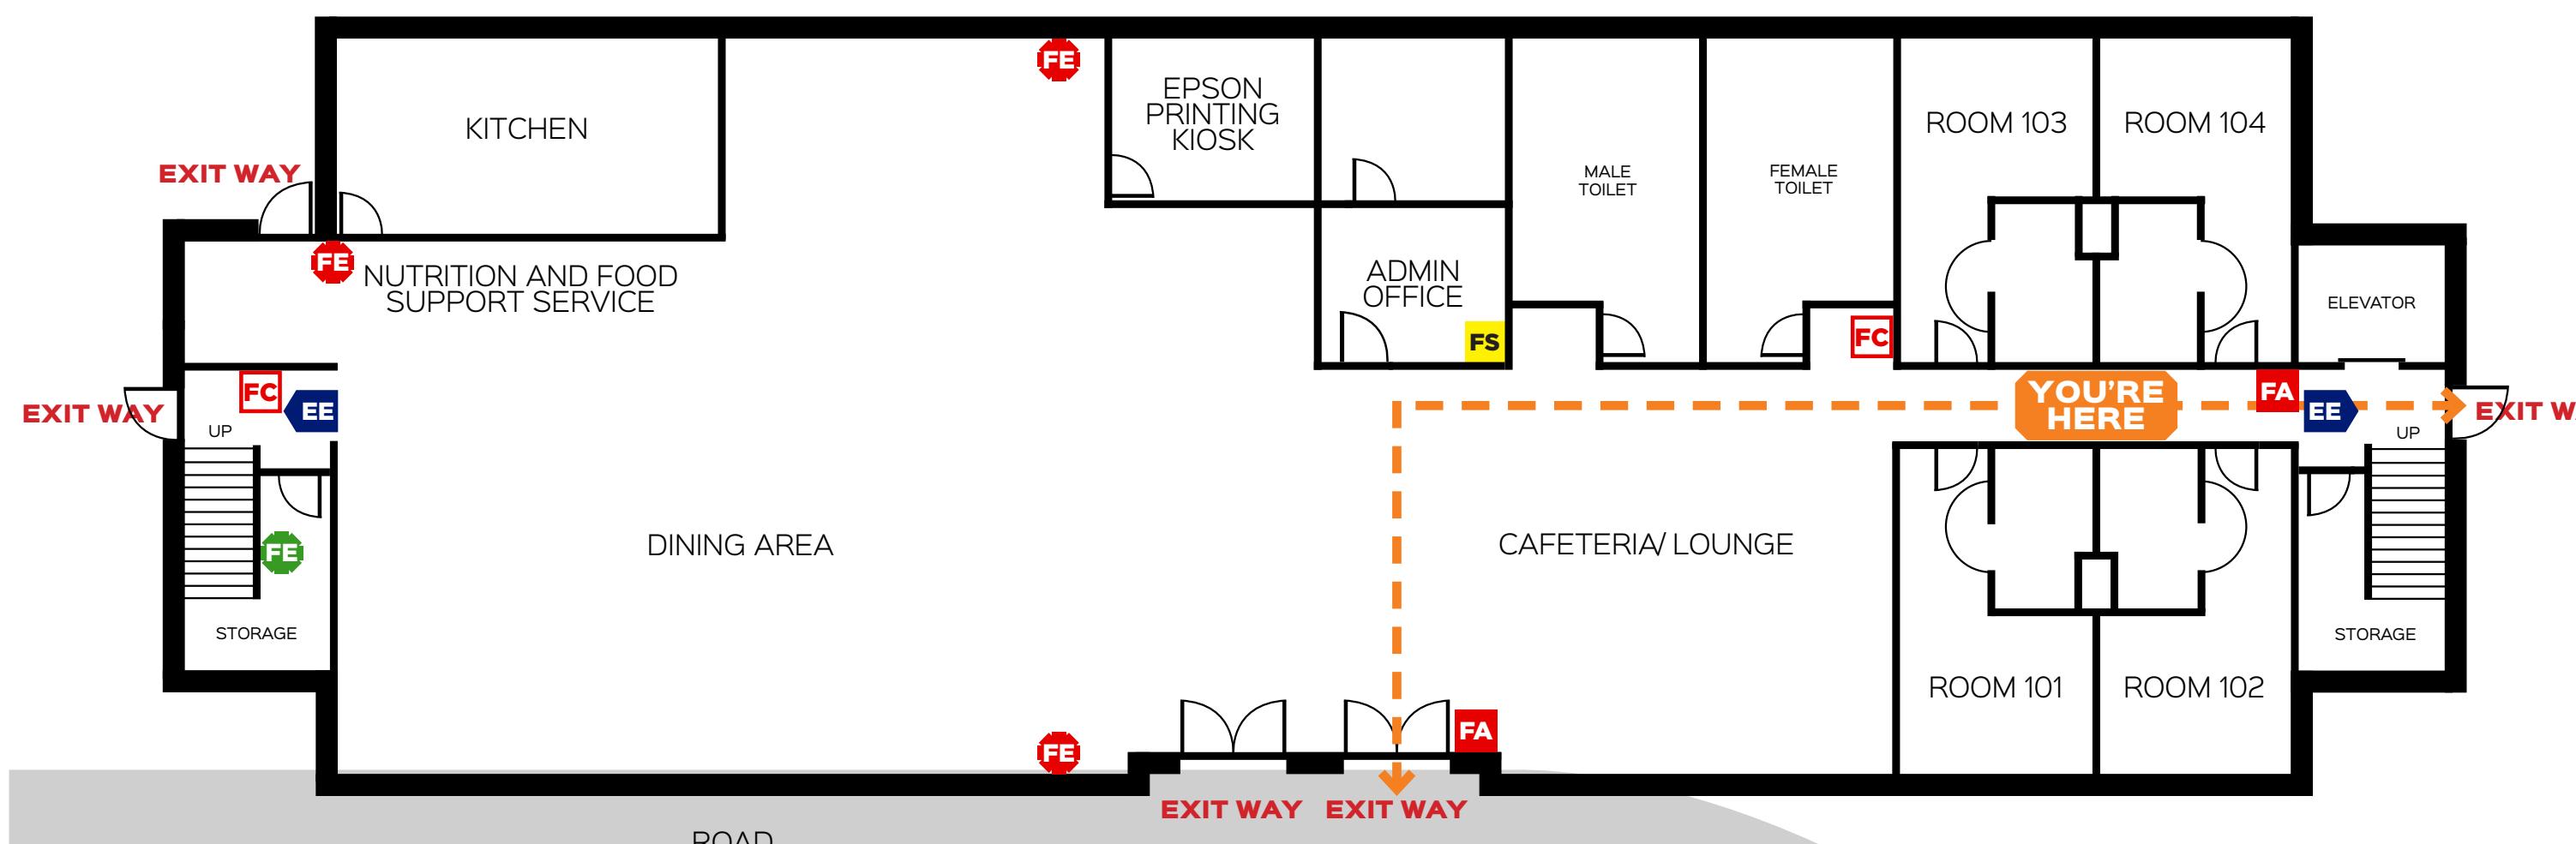

#### LEGEND



**FE** FIRE EXTINGUISHER



**FC**

FIRE HOSE CABINET



**YOU'RE HERE**


CURRENT LOCATION



**FA** FIRE ALARM



**FH** FIRE HYDRANT

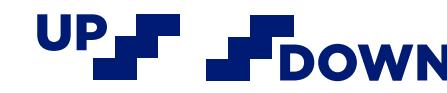

**UP** **DOWN** STAIRS



**FA** FIRST AID KIT



**FS** FDAS PANEL




**EE** EMERGENCY EXIT



**DIRECTIONAL EXIT SIGNS**

#### ■ ASSEMBLY AREA

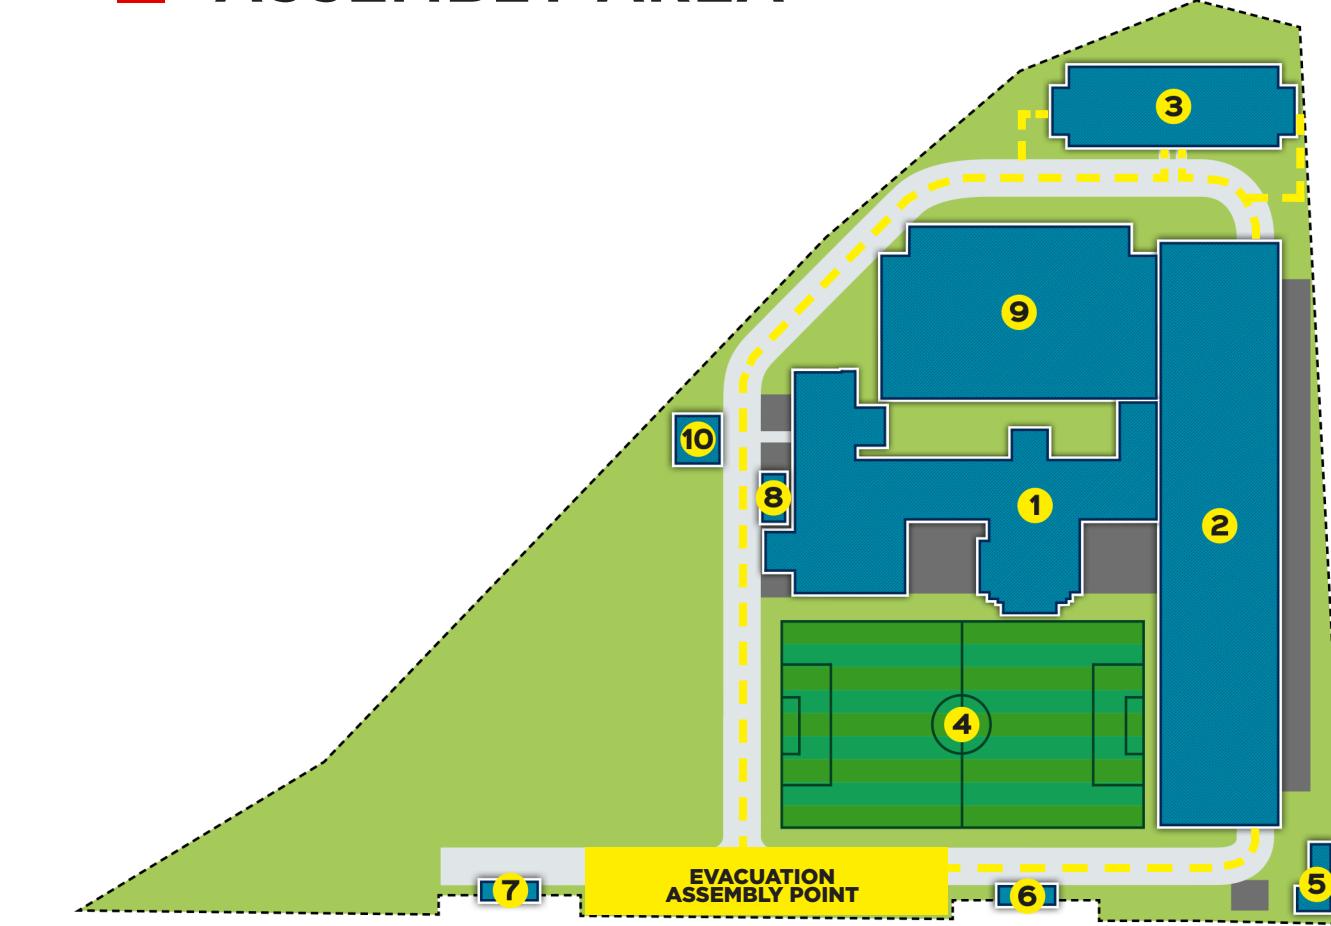

#### ■ IN CASE OF EMERGENCY

- Remain calm, do not panic.
- Remove all persons from danger.
- In case of emergency, do not use the elevator. Leave the building using the nearest fire exit route.
- WALK, DO NOT RUN.
- Activate fire alarm.

#### ■ ASSEMBLY AREA REMINDERS

- Account for persons missing from the building.
- Report any missing persons to the emergency response team.
- DO NOT re-enter the building until the "ALL CLEAR" is given by the responding emergency service.

#### ■ EMERGENCY NUMBERS

CLINIC	(63) 998 961 1923
PFMO/ SECURITY	(63) 998 988 1908
FIRE	(63) 945 490 4131
POLICE	(049) 545 1698
CDRRMO & POSO	(63) 917 148 9813
AMBULANCE	(049) 545 1740

# EVACUATION MAP

## GROUND FLOOR DORMITEL

### CAFETERIA/ LOUNGE AREA



#### LEGEND



**FE** FIRE EXTINGUISHER



**FC** FIRE HOSE CABINET



**YOU'RE HERE** CURRENT LOCATION



**FA**

FIRE ALARM

**EE** EMERGENCY EXIT



**FH**

FIRE HYDRANT



**UP**

**DOWN**

STAIRS



**FA**

FIRST AID KIT



— — →

← — —


DIRECTIONAL EXIT SIGNS



**FS**

FDAS PANEL

#### ■ ASSEMBLY AREA

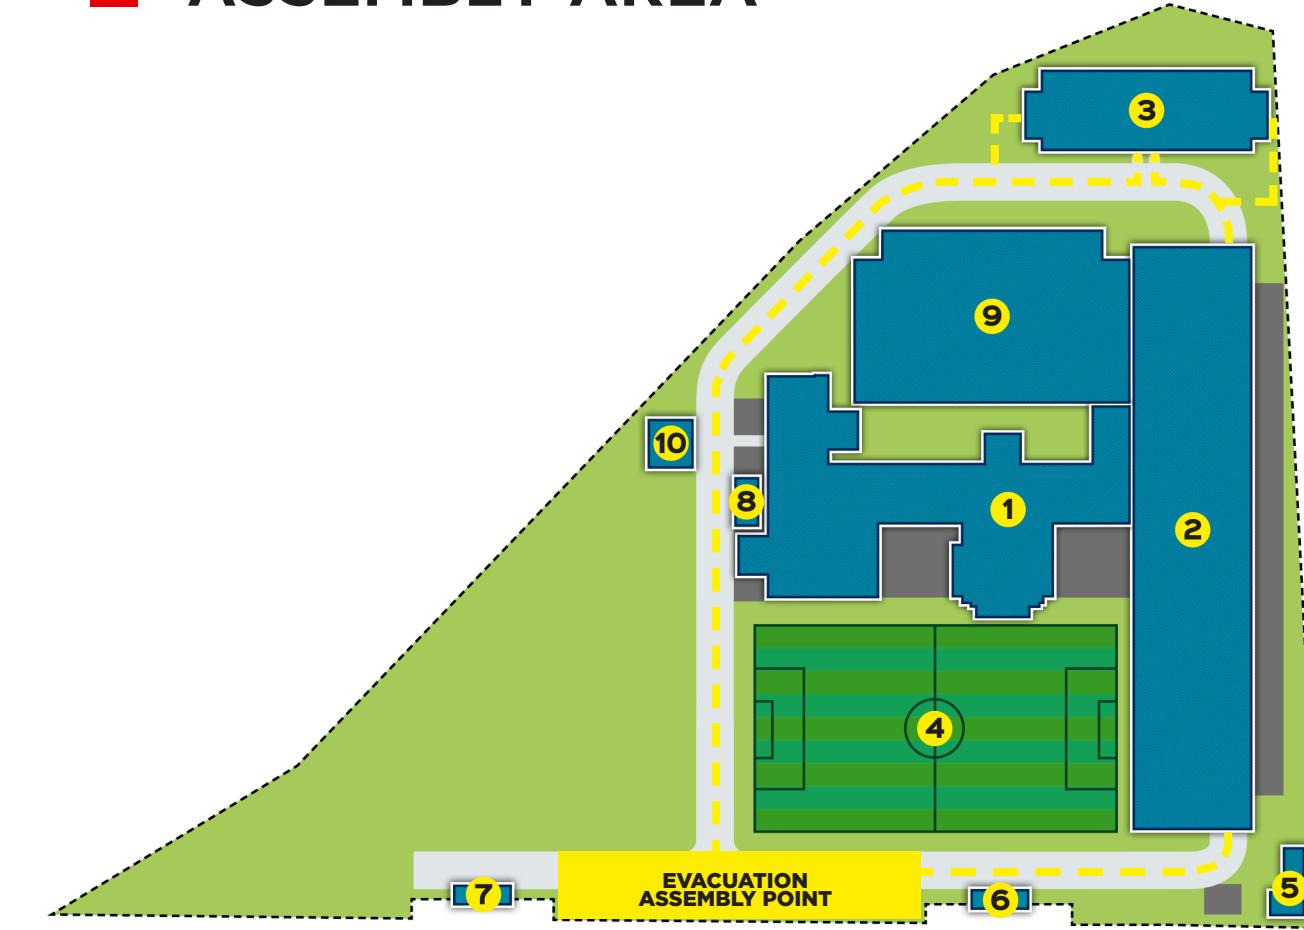

#### ■ IN CASE OF EMERGENCY

- Remain calm, do not panic.
- Remove all persons from danger.
- In case of emergency, do not use the elevator. Leave the building using the nearest fire exit route.
- WALK, DO NOT RUN.
- Activate fire alarm.

#### ■ ASSEMBLY AREA REMINDERS

- Account for persons missing from the building.
- Report any missing persons to the emergency response team.
- DO NOT re-enter the building until the "ALL CLEAR" is given by the responding emergency service.


#### ■ EMERGENCY NUMBERS

CLINIC	(63) 998 961 1923
PFMO/ SECURITY	(63) 998 988 1908
FIRE	(63) 945 490 4131
POLICE	(049) 545 1698
CDRRMO & POSO	(63) 917 148 9813
AMBULANCE	(049) 545 1740

# EVACUATION MAP

## GROUND FLOOR DORMITEL

### DINING AREA

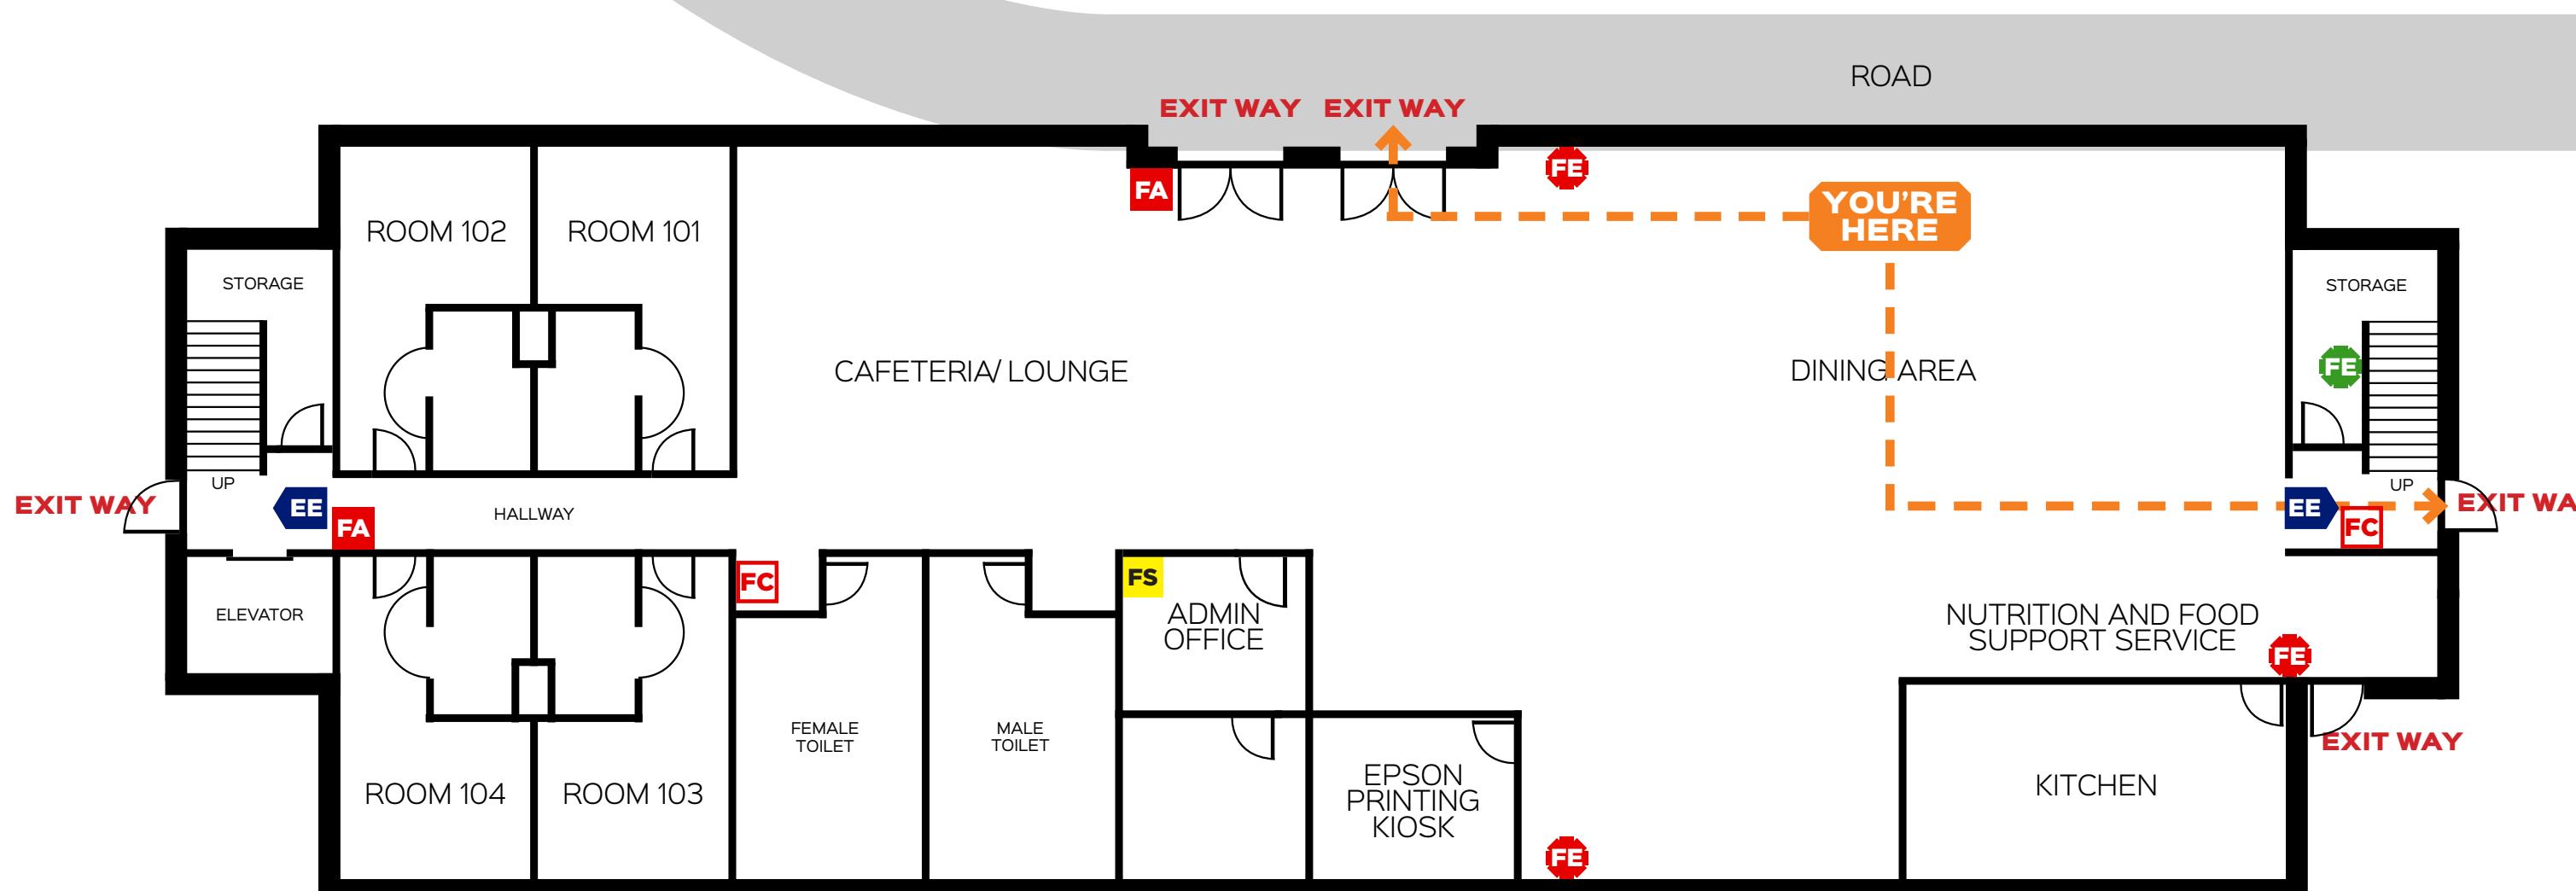

#### LEGEND



**FIRE EXTINGUISHER**



**FIRE ALARM**



**EMERGENCY EXIT**



**FIRE HOSE CABINET**



**FIRE HYDRANT**



**UP** **DOWN** **STAIRS**



**FIRST AID KIT**



**CURRENT LOCATION**




**DIRECTIONAL EXIT SIGNS**



**FDAS PANEL**

#### ■ ASSEMBLY AREA

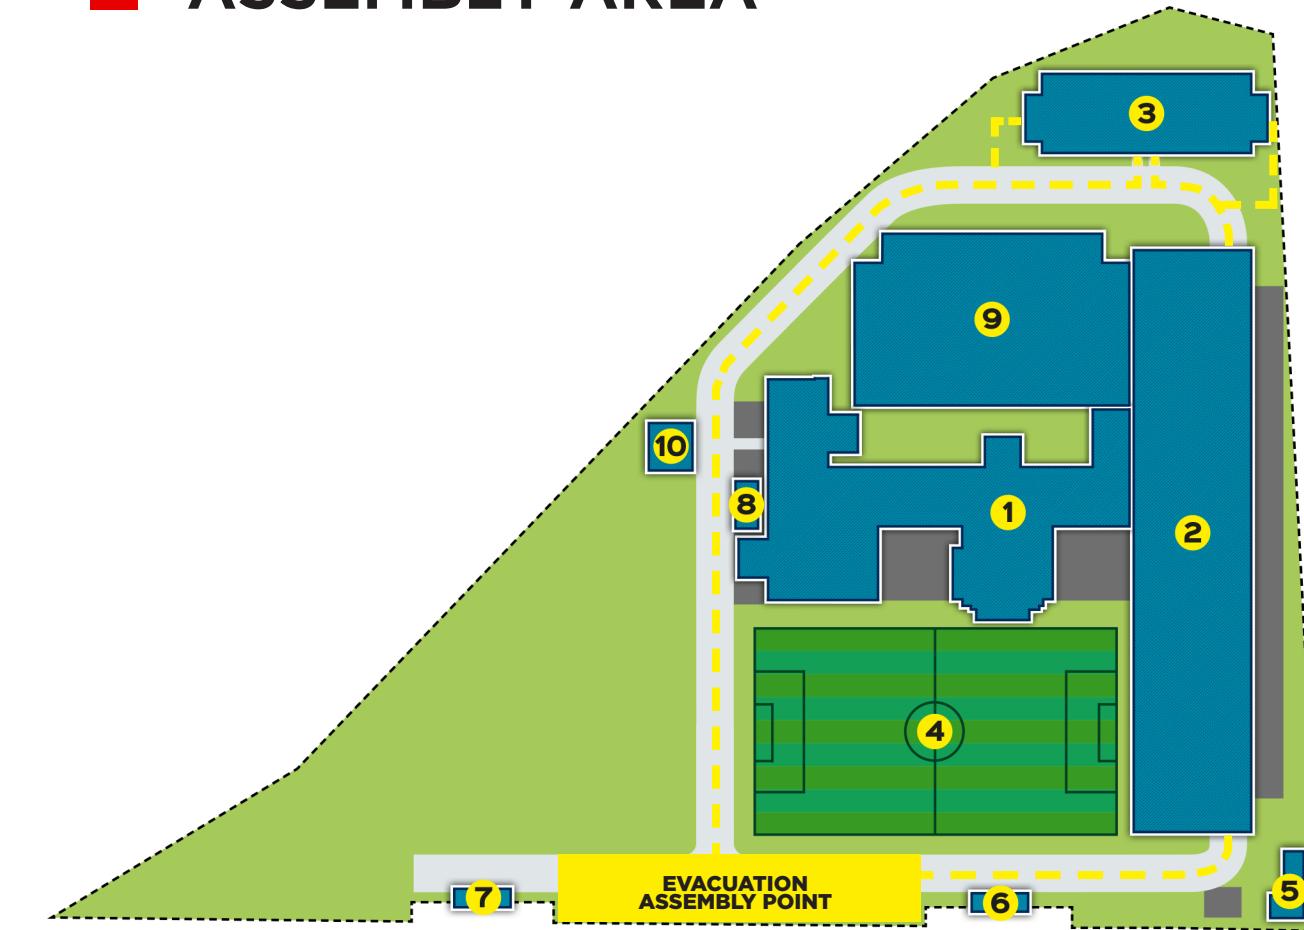

#### ■ IN CASE OF EMERGENCY

- Remain calm, do not panic.
- Remove all persons from danger.
- In case of emergency, do not use the elevator. Leave the building using the nearest fire exit route.
- WALK, DO NOT RUN.
- Activate fire alarm.

#### ■ ASSEMBLY AREA REMINDERS

- Account for persons missing from the building.
- Report any missing persons to the emergency response team.
- DO NOT re-enter the building until the "ALL CLEAR" is given by the responding emergency service.


#### ■ EMERGENCY NUMBERS

CLINIC	(63) 998 961 1923
PFMO/ SECURITY	(63) 998 988 1908
FIRE	(63) 945 490 4131
POLICE	(049) 545 1698
CDRRMO & POSO	(63) 917 148 9813
AMBULANCE	(049) 545 1740

# EVACUATION MAP

## GROUND FLOOR DORMITEL

### KITCHEN AREA

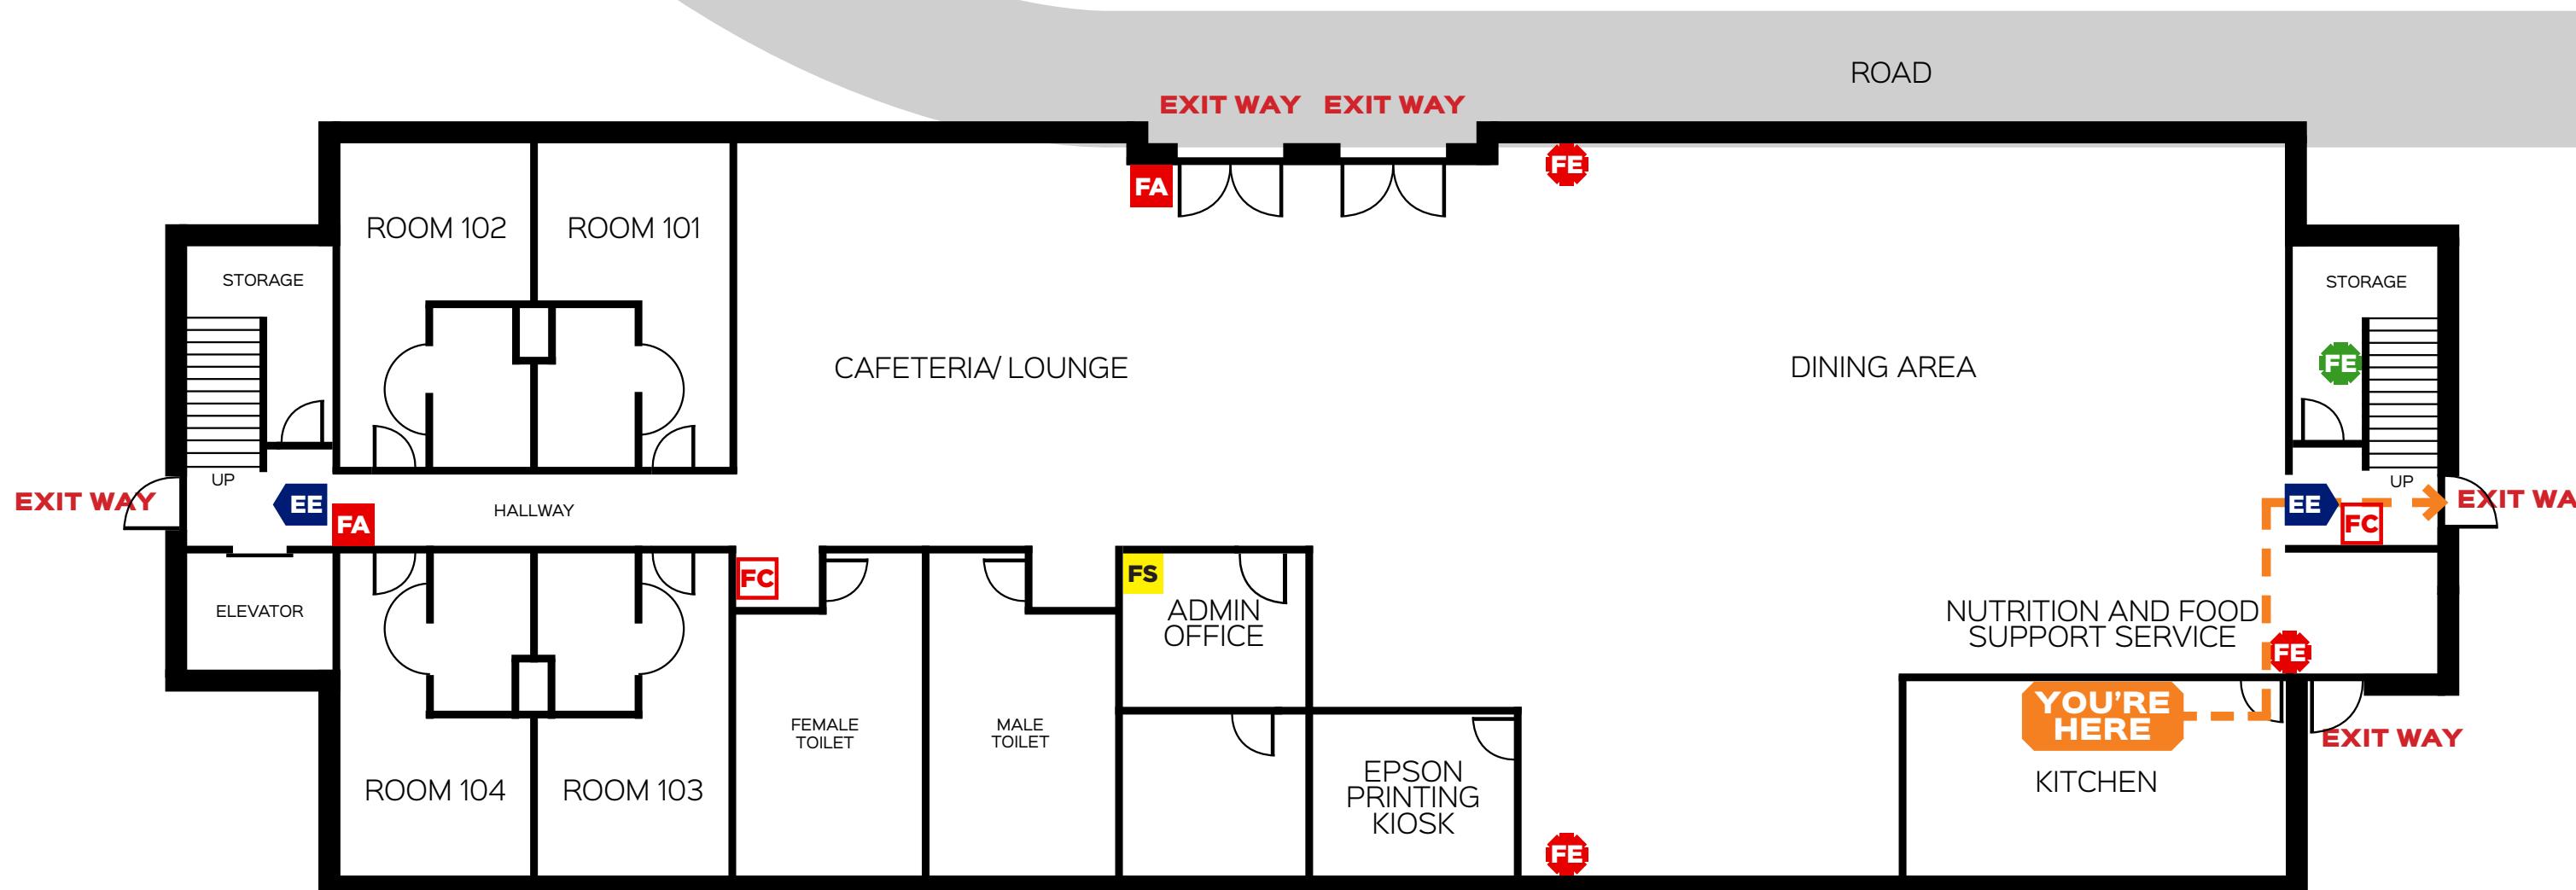

#### LEGEND



**FIRE EXTINGUISHER**



**FIRE ALARM**



**EMERGENCY EXIT**



**FIRE HOSE CABINET**



**FIRE HYDRANT**



**UP ↓ DOWN STAIRS**



**FIRST AID KIT**



**CURRENT LOCATION**




**DIRECTIONAL EXIT SIGNS**



**FDAS PANEL**

#### ■ ASSEMBLY AREA

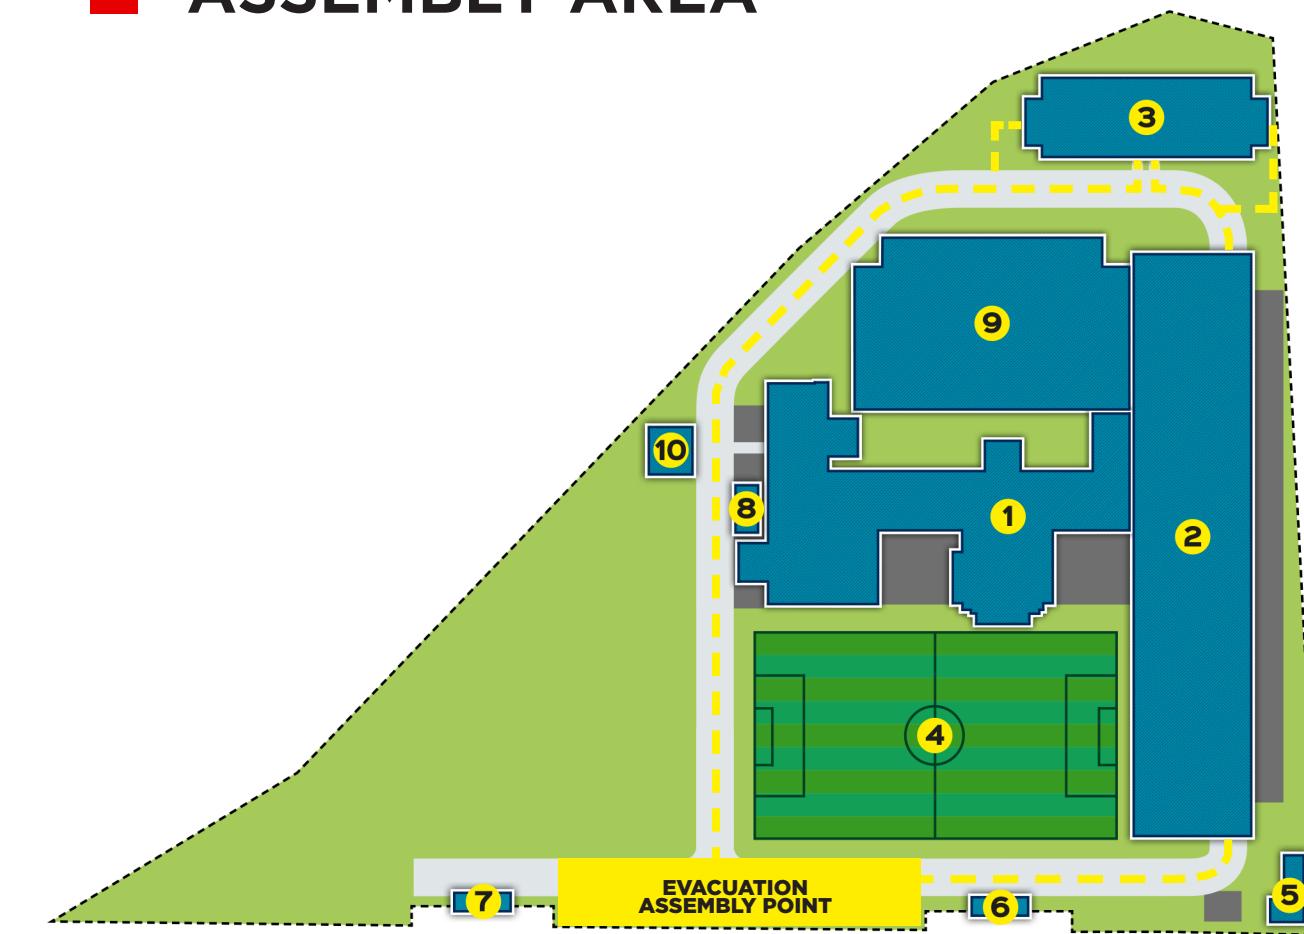

#### ■ IN CASE OF EMERGENCY

- Remain calm, do not panic.
- Remove all persons from danger.
- In case of emergency, do not use the elevator. Leave the building using the nearest fire exit route.
- WALK, DO NOT RUN.
- Activate fire alarm.

#### ■ ASSEMBLY AREA REMINDERS

- Account for persons missing from the building.
- Report any missing persons to the emergency response team.
- DO NOT re-enter the building until the "ALL CLEAR" is given by the responding emergency service.

#### ■ EMERGENCY NUMBERS


CLINIC	(63) 998 961 1923
PFMO/ SECURITY	(63) 998 988 1908
FIRE	(63) 945 490 4131
POLICE	(049) 545 1698
CDRRMO & POSO	(63) 917 148 9813
AMBULANCE	(049) 545 1740

**SECOND FLOOR**

# EVACUATION MAP

## SECOND FLOOR DORMITEL

### HALLWAY IN BETWEEN ROOM 212 AND ROOM 213

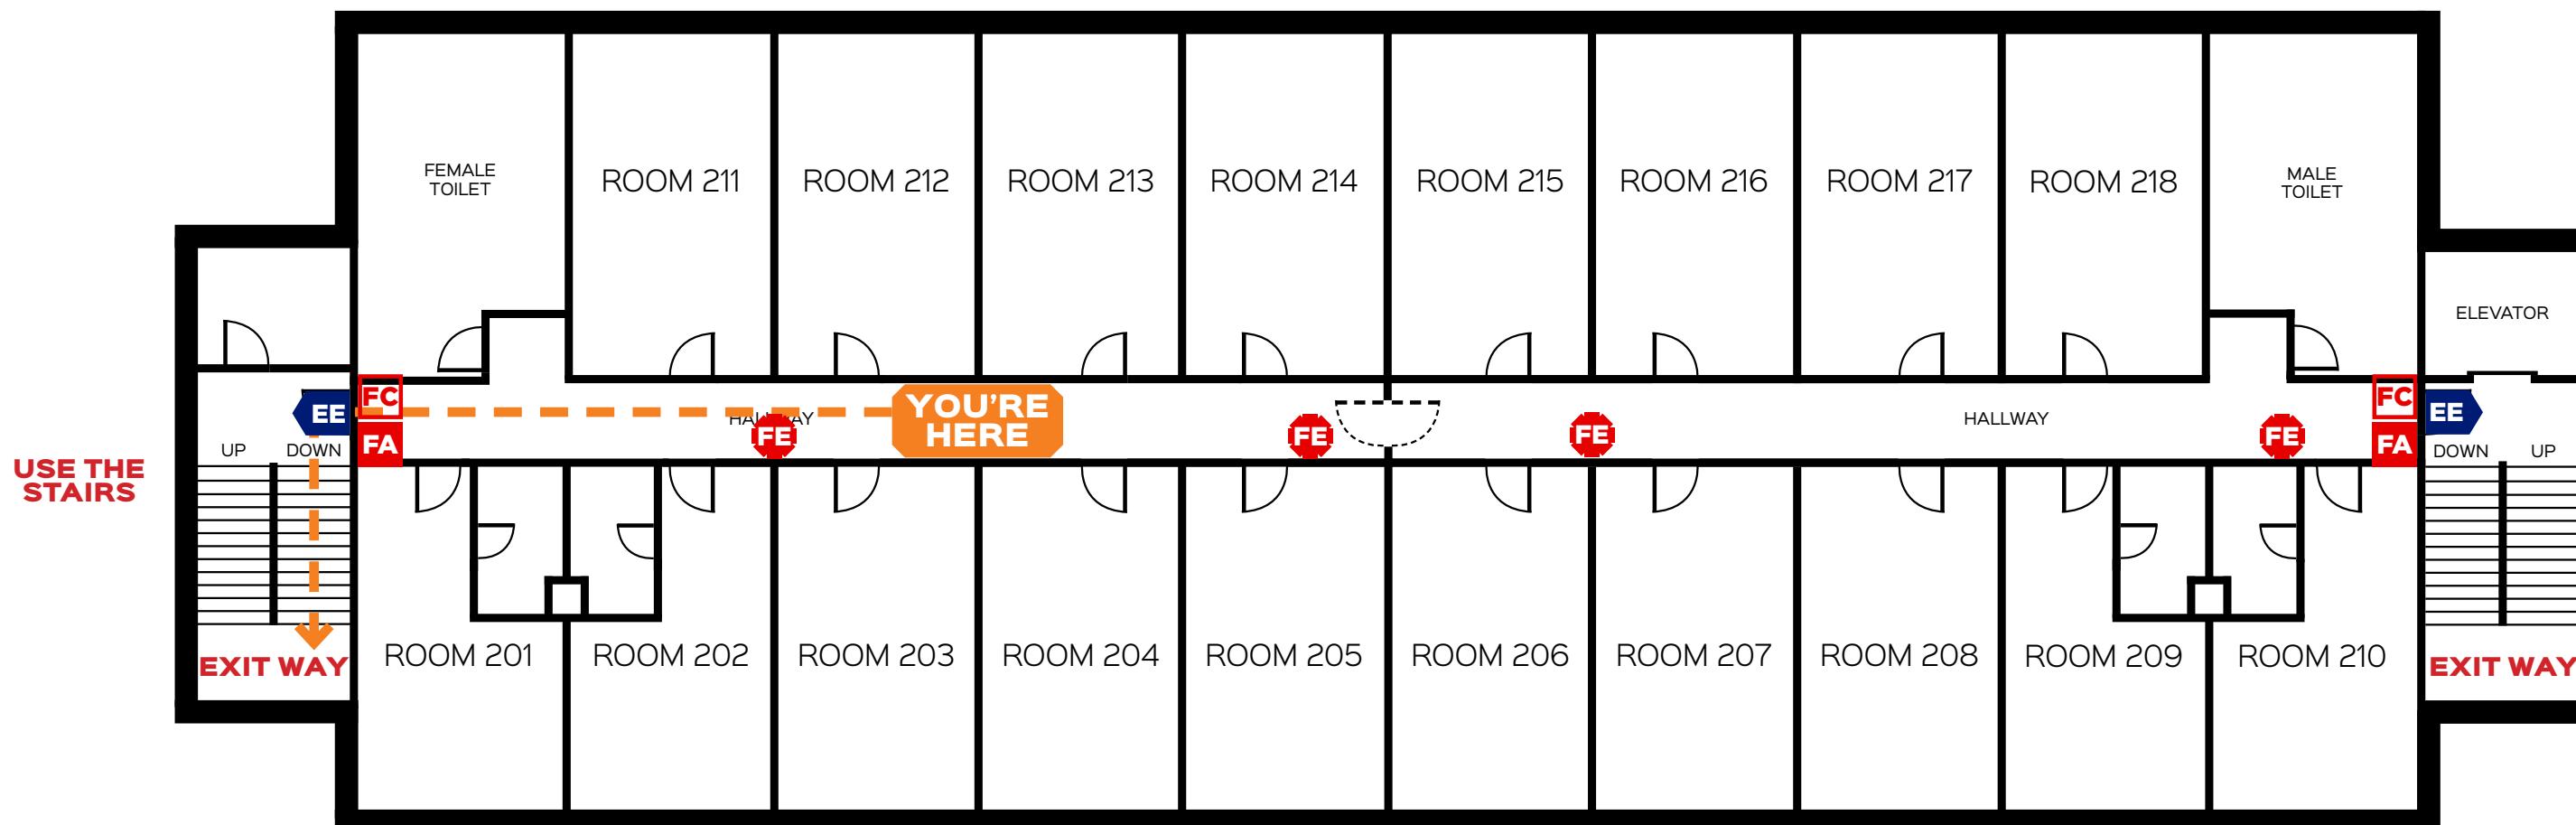

#### LEGEND



FE FIRE EXTINGUISHER



FA FIRE ALARM



EMERGENCY EXIT



FC FIRE HOSE CABINET

FH FIRE HYDRANT



UP STAIRS



DOWN STAIRS



FA FIRST AID KIT




CURRENT LOCATION

—→ ← — DIRECTIONAL EXIT SIGNS



FS FDAS PANEL

#### ■ ASSEMBLY AREA

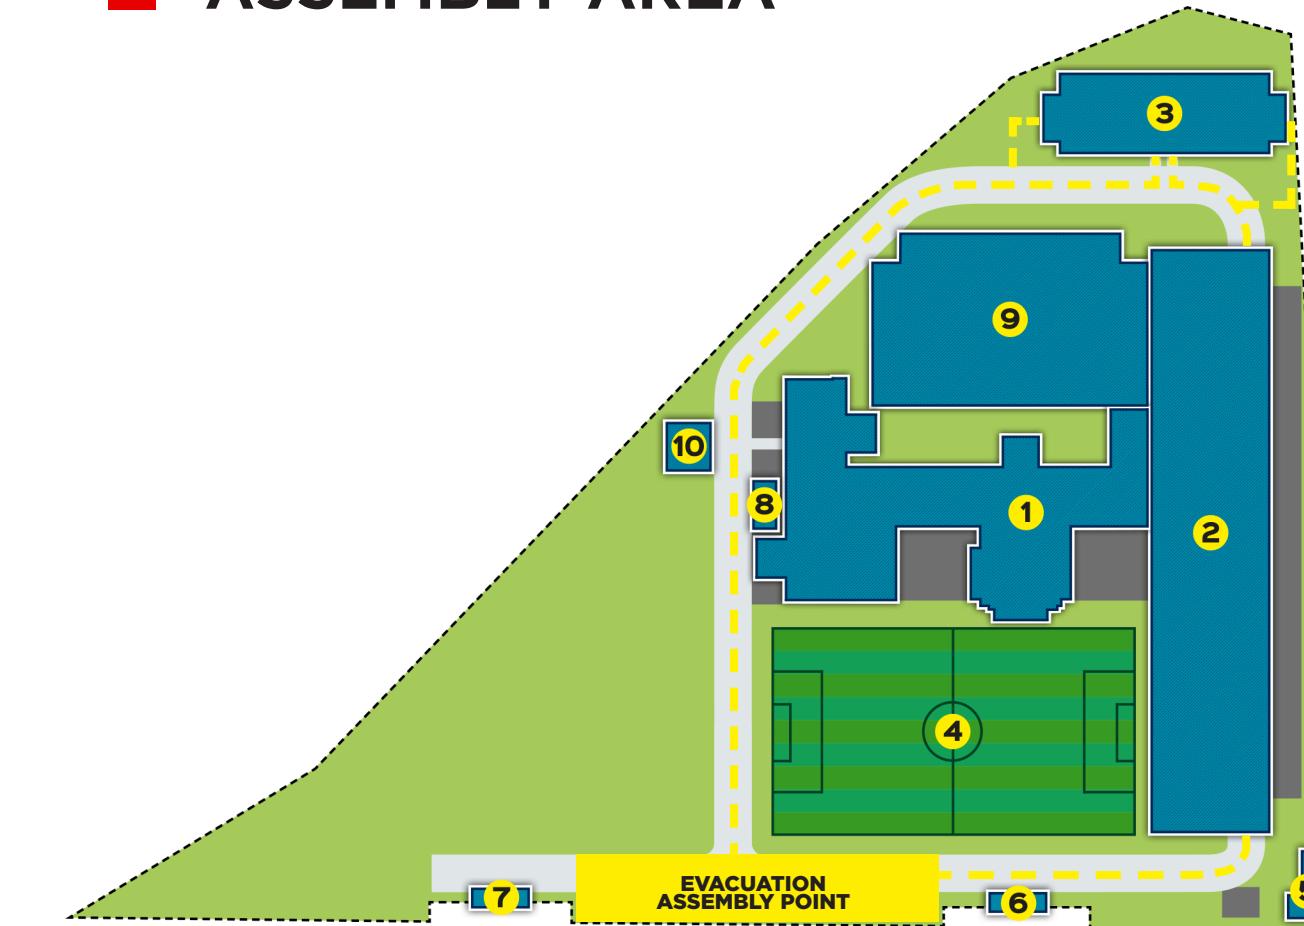

#### ■ IN CASE OF EMERGENCY

- Remain calm, do not panic.
- Remove all persons from danger.
- In case of emergency, do not use the elevator. Leave the building using the nearest fire exit route.
- WALK, DO NOT RUN.
- Activate fire alarm.

#### ■ ASSEMBLY AREA REMINDERS

- Account for persons missing from the building.
- Report any missing persons to the emergency response team.
- DO NOT re-enter the building until the "ALL CLEAR" is given by the responding emergency service.


#### ■ EMERGENCY NUMBERS

CLINIC	(63) 998 961 1923
PFMO/ SECURITY	(63) 998 988 1908
FIRE	(63) 945 490 4131
POLICE	(049) 545 1698
CDRRMO & POSO	(63) 917 148 9813
AMBULANCE	(049) 545 1740

# EVACUATION MAP

## SECOND FLOOR DORMITEL

### HALLWAY IN BETWEEN ROOM 207 AND ROOM 208

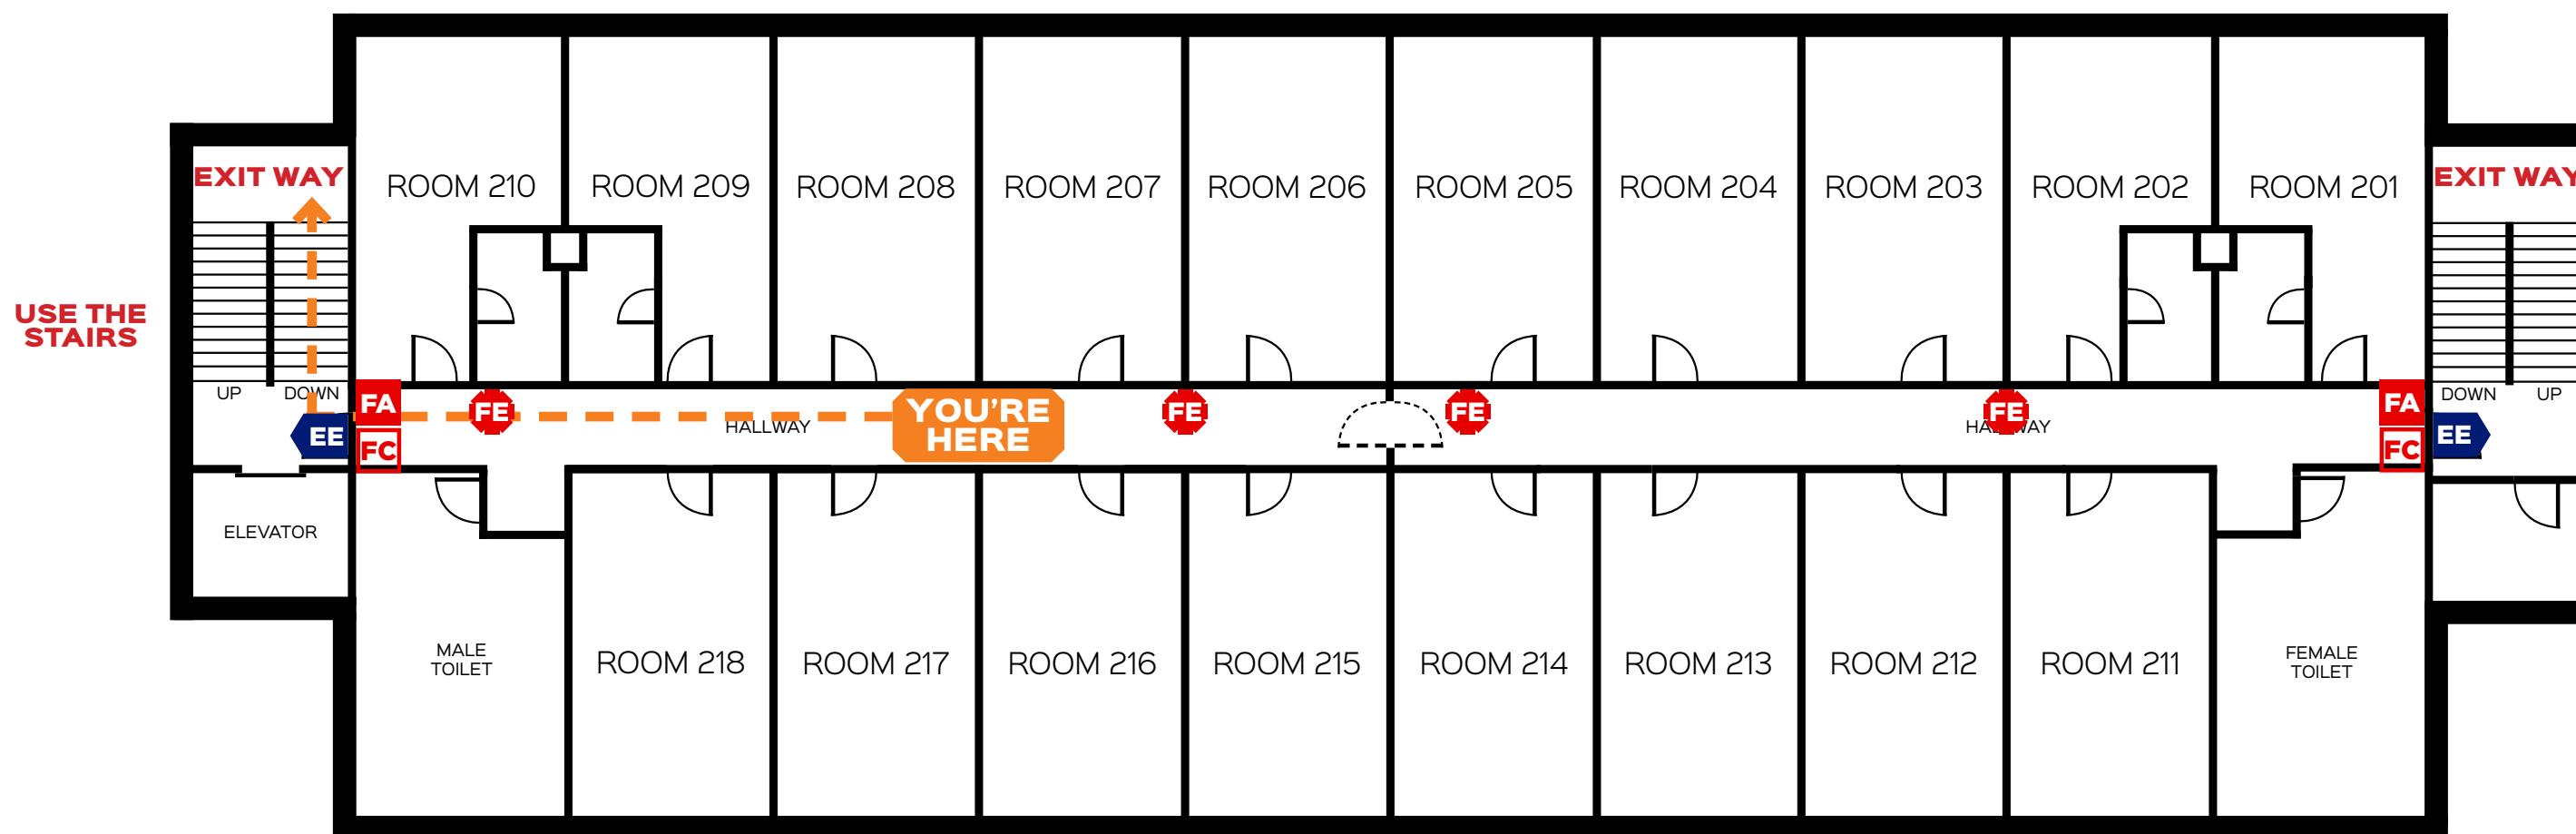

#### LEGEND



FA FIRE ALARM



EMERGENCY EXIT



FH FIRE HYDRANT



UP DOWN STAIRS



FIRST AID KIT



CURRENT LOCATION




DIRECTIONAL EXIT SIGNS



FDAS PANEL

#### ■ ASSEMBLY AREA

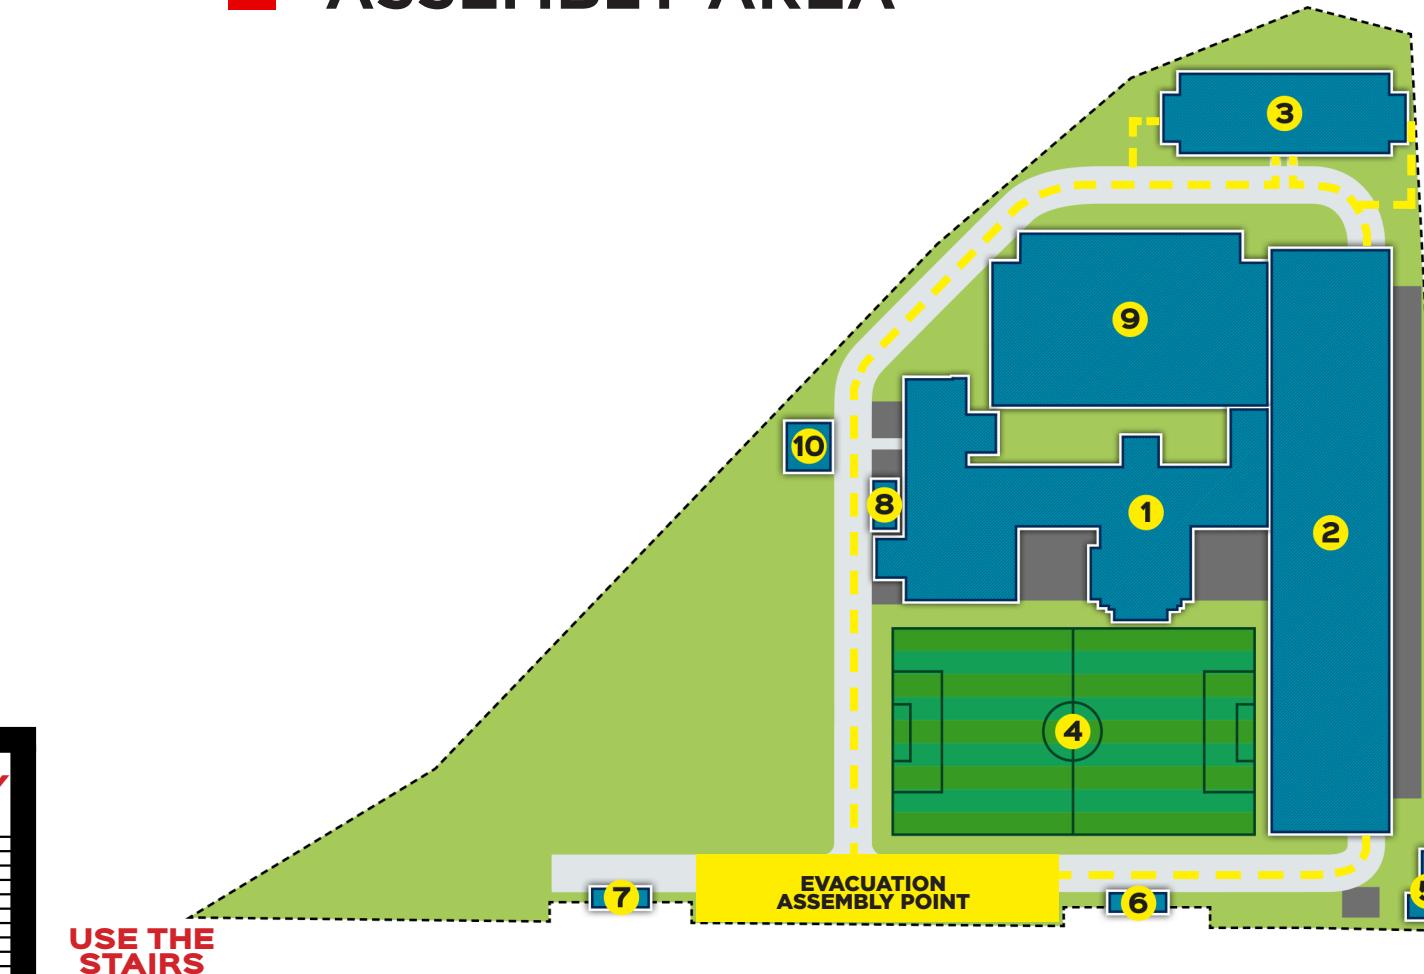

#### ■ IN CASE OF EMERGENCY

- Remain calm, do not panic.
- Remove all persons from danger.
- In case of emergency, do not use the elevator. Leave the building using the nearest fire exit route.
- WALK, DO NOT RUN.
- Activate fire alarm.

#### ■ ASSEMBLY AREA REMINDERS

- Account for persons missing from the building.
- Report any missing persons to the emergency response team.
- DO NOT re-enter the building until the "ALL CLEAR" is given by the responding emergency service.

#### ■ EMERGENCY NUMBERS

CLINIC	(63) 998 961 1923
PFMO/ SECURITY	(63) 998 988 1908
FIRE	(63) 945 490 4131
POLICE	(049) 545 1698
CDRRMO & POSO	(63) 917 148 9813
AMBULANCE	(049) 545 1740


**THIRD FLOOR**

# EVACUATION MAP

# **THIRD FLOOR**

## **DORMITEL**

# HALLWAY IN BETWEEN ROOM 312 AND ROOM 313

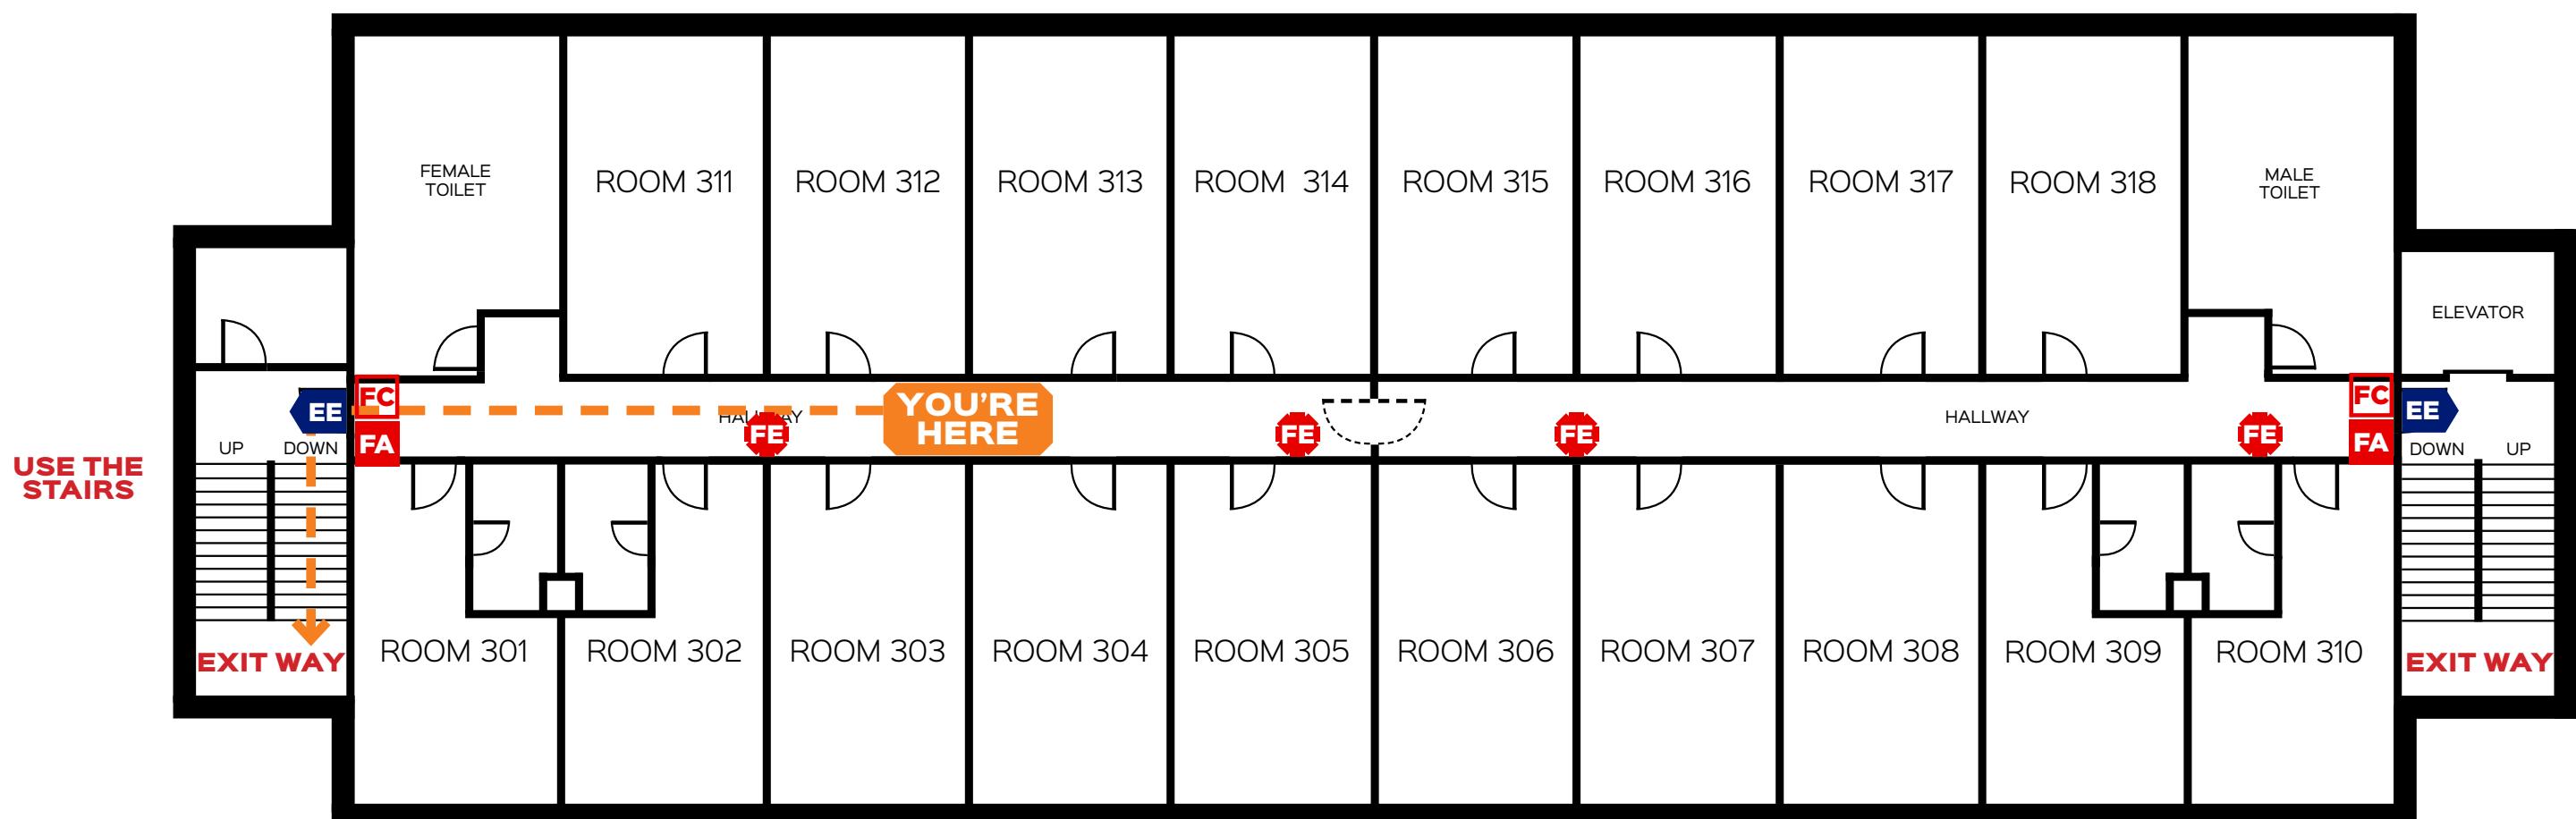

## LEGEND



# **FA FIRE ALARM**



# **FH FIRE HYDRANT**



 **FIRST AID KIT**




# CURRENT LOCATION



◀ — — DIRECTIONAL EXIT SIGNS



# AS PANEL

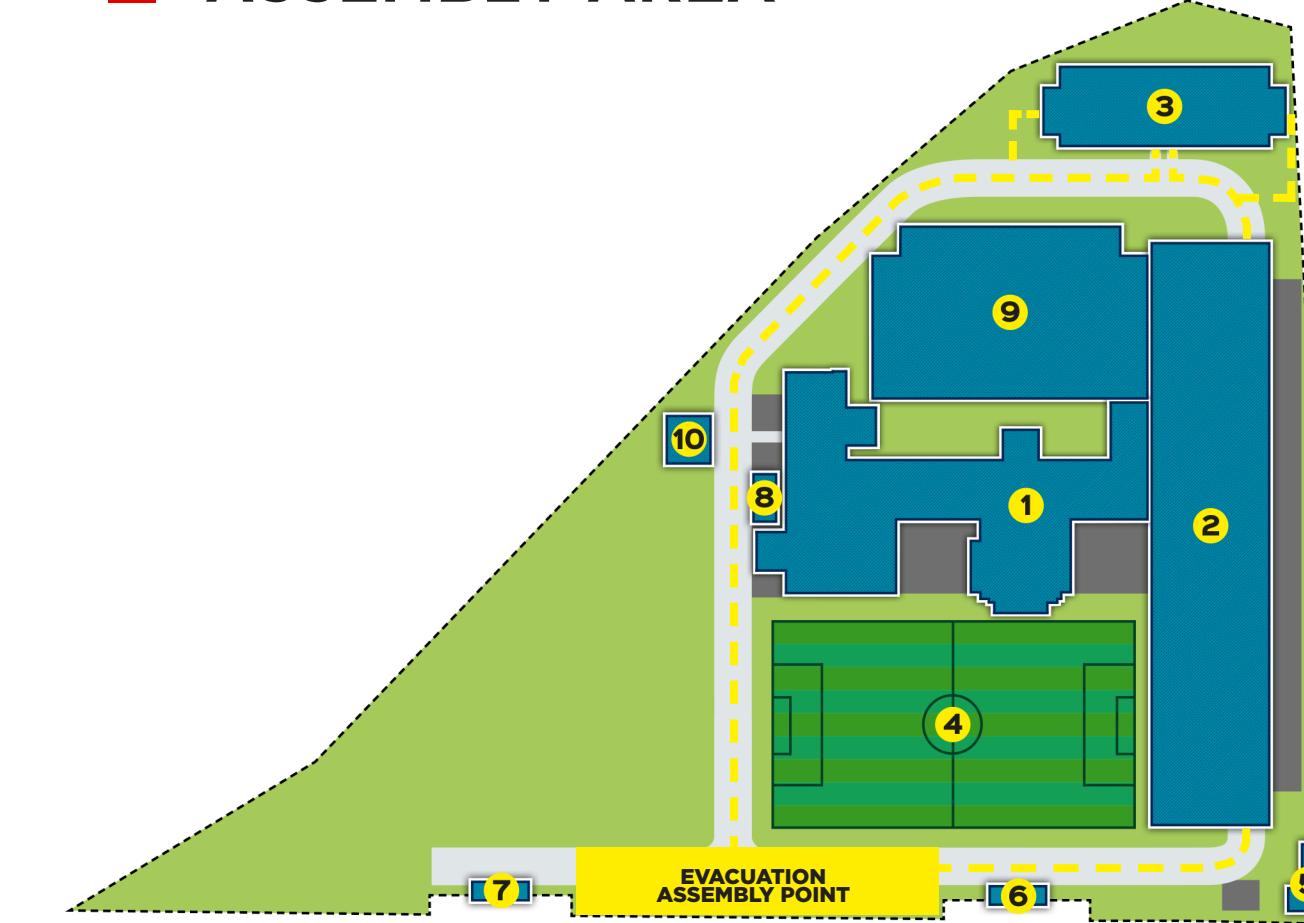

## **IN CASE OF EMERGENCY**

- Remain calm, do not panic.
  - Remove all persons from danger.
  - In case of emergency, do not use the elevator. Leave the building using the nearest fire exit route.
  - WALK, DO NOT RUN.
  - Activate fire alarm.



# ASSEMBLY AREA REMINDERS

- Account for persons missing from the building.
  - Report any missing persons to the emergency response team.
  - DO NOT re-enter the building until the “ALL CLEAR” is given by the responding emergency service.

# ■ EMERGENCY NUMBERS


**CLINIC** (63) 998 961 1923  
**PFMO/ SECURITY** (63) 998 988 1908  
**FIRE** (63) 945 490 4131  
**POLICE** (049) 545 1698  
**CDRRMO & POSO** (63) 917 148 9813  
**AMBULANCE** (049) 545 1740

# EVACUATION MAP

# **THIRD FLOOR**

## **DORMITEL**

# HALLWAY IN BETWEEN ROOM 307 AND ROOM 308

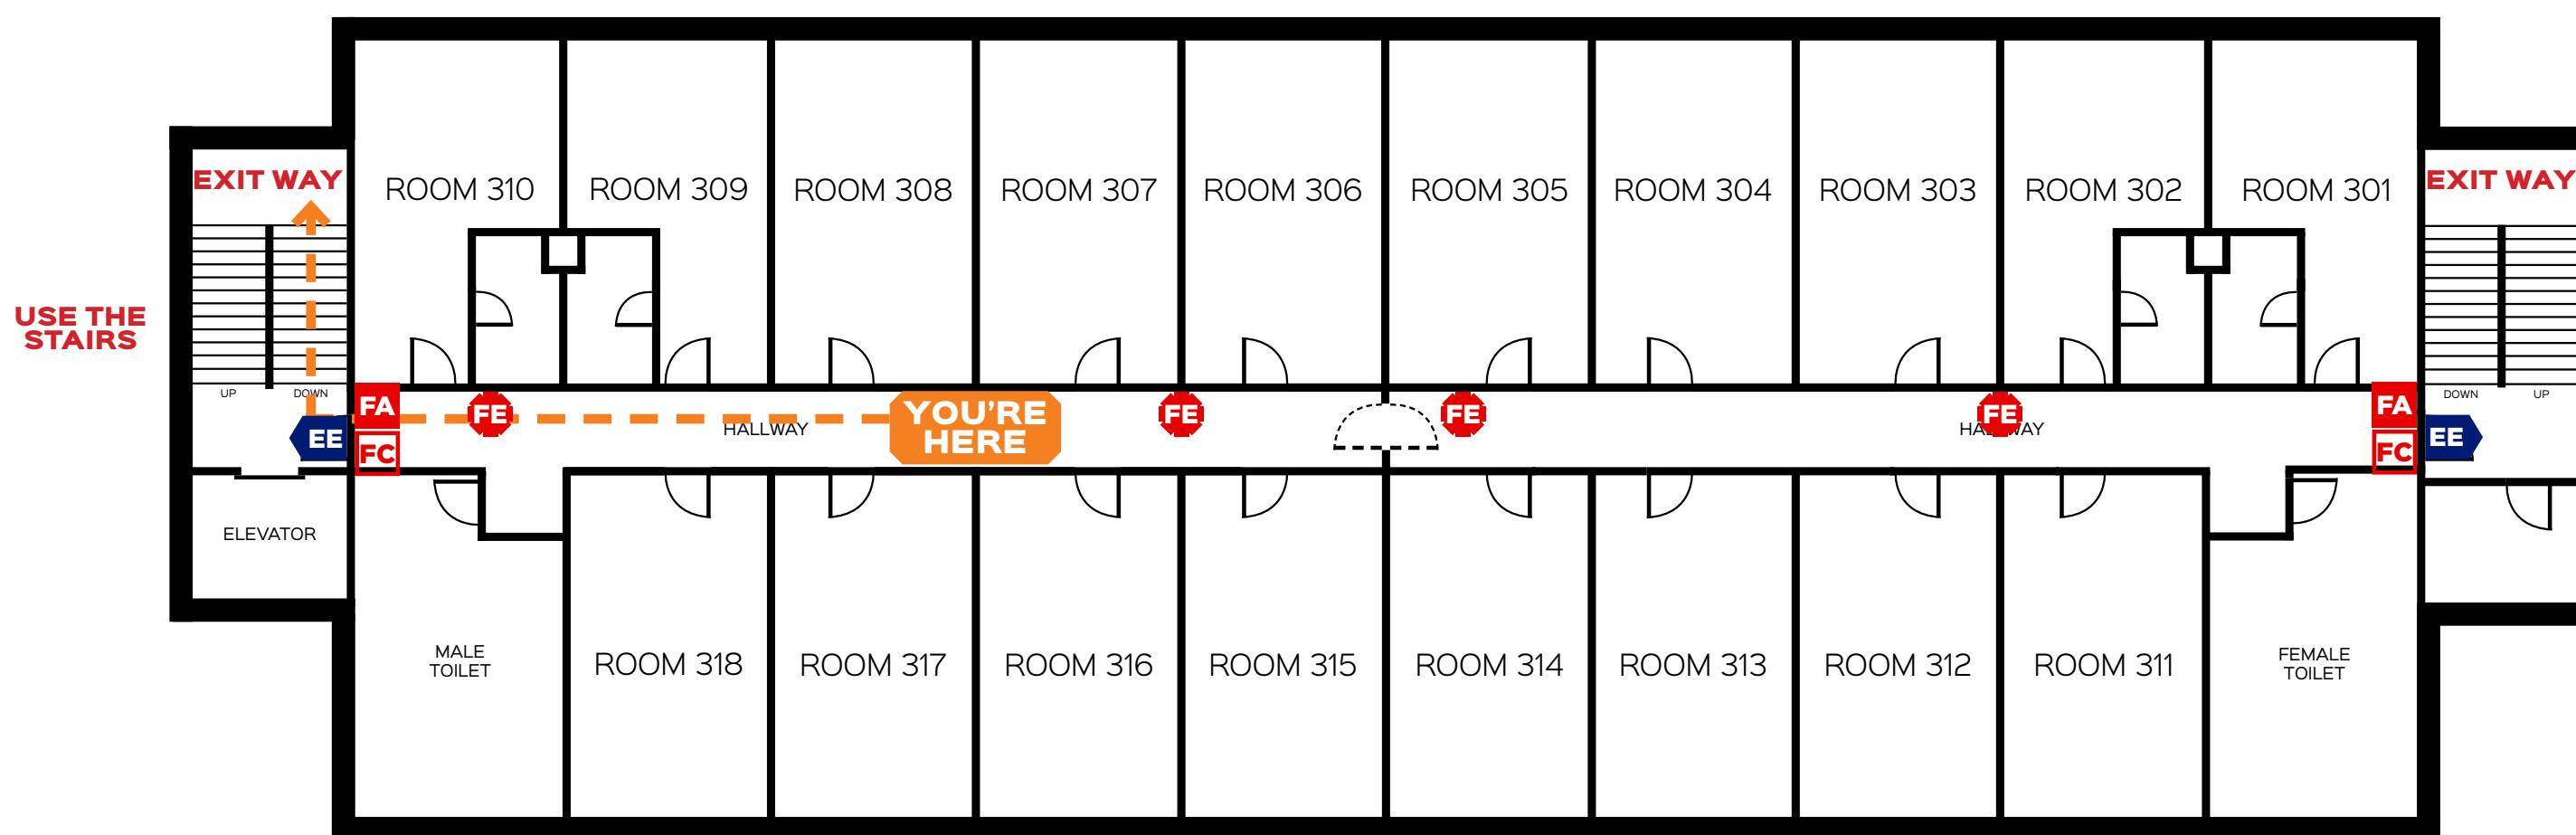

## LEGEND



**FA FIRE ALARM**



 FIRE HYDRANT




# YOU'RE HERE

# CURRENT LOCATION



**FDAS PANEL**

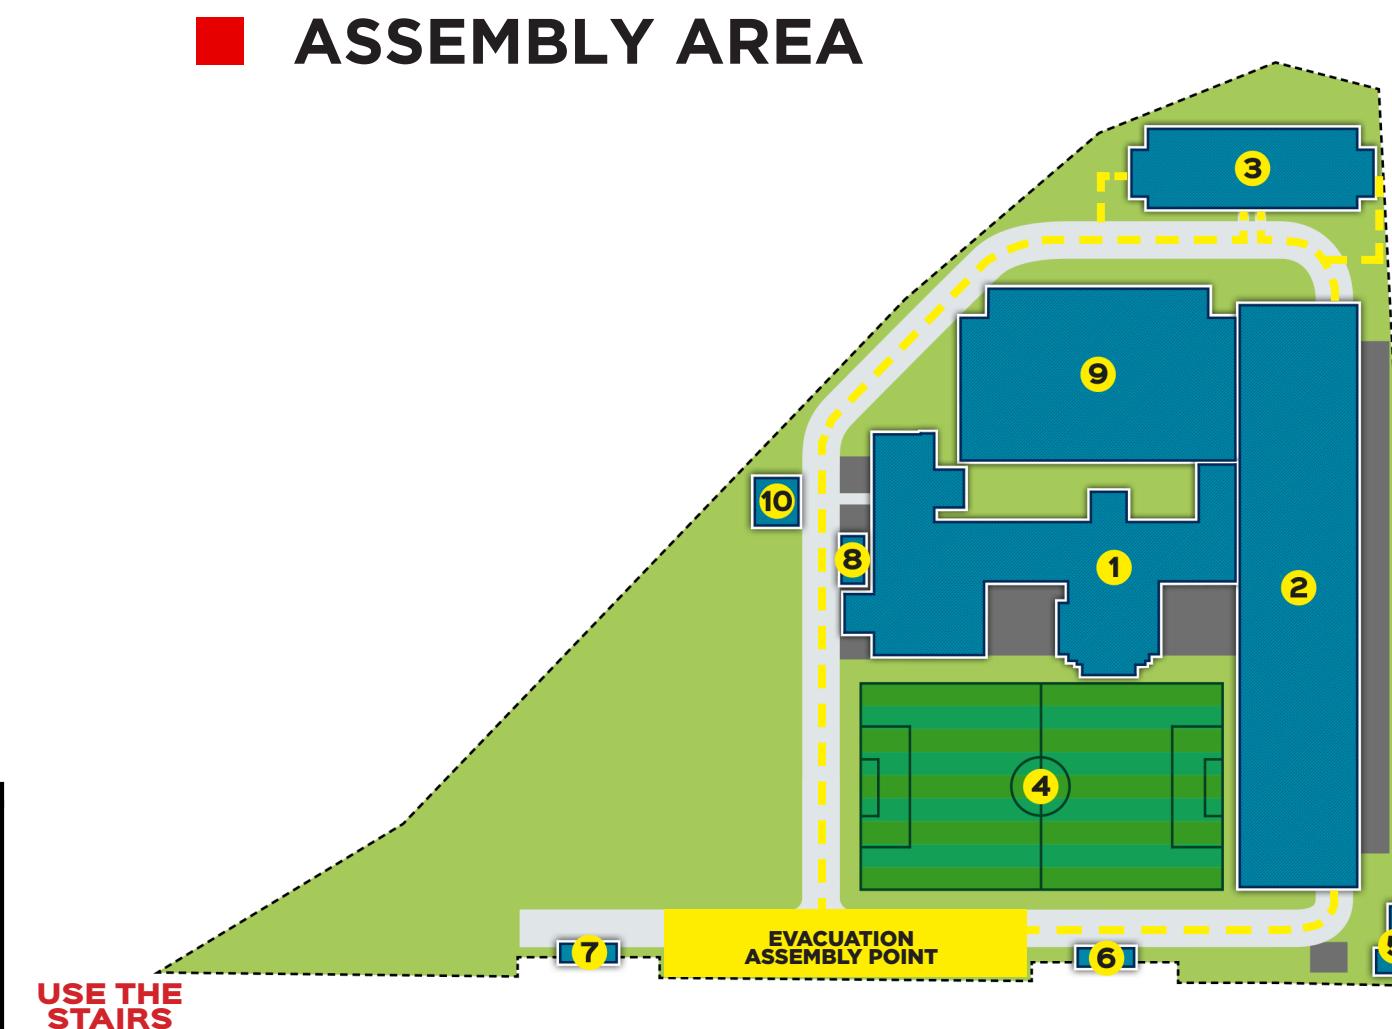

## IN CASE OF EMERGENCY

- Remain calm, do not panic.
  - Remove all persons from danger.
  - In case of emergency, do not use the elevator. Leave the building using the nearest fire exit route.
  - WALK, DO NOT RUN.
  - Activate fire alarm.

# ASSEMBLY AREA REMINDERS

- Account for persons missing from the building.
  - Report any missing persons to the emergency response team.
  - DO NOT re-enter the building until the “ALL CLEAR” is given by the responding emergency service.

# ■ EMERGENCY NUMBERS

<b>CLINIC</b>	<b>(63) 998 961 1923</b>
<b>PFMO/ SECURITY</b>	<b>(63) 998 988 1908</b>
<b>FIRE</b>	<b>(63) 945 490 4131</b>
<b>POLICE</b>	<b>(049) 545 1698</b>
<b>CDRRMO &amp; POSO</b>	<b>(63) 917 148 9813</b>
<b>AMBULANCE</b>	<b>(049) 545 1740</b>


**FOURTH FLOOR**

# EVACUATION MAP

# **FOURTH FLOOR**

## **DORMITEL**

# HALLWAY IN BETWEEN ROOM 413 AND ROOM 414

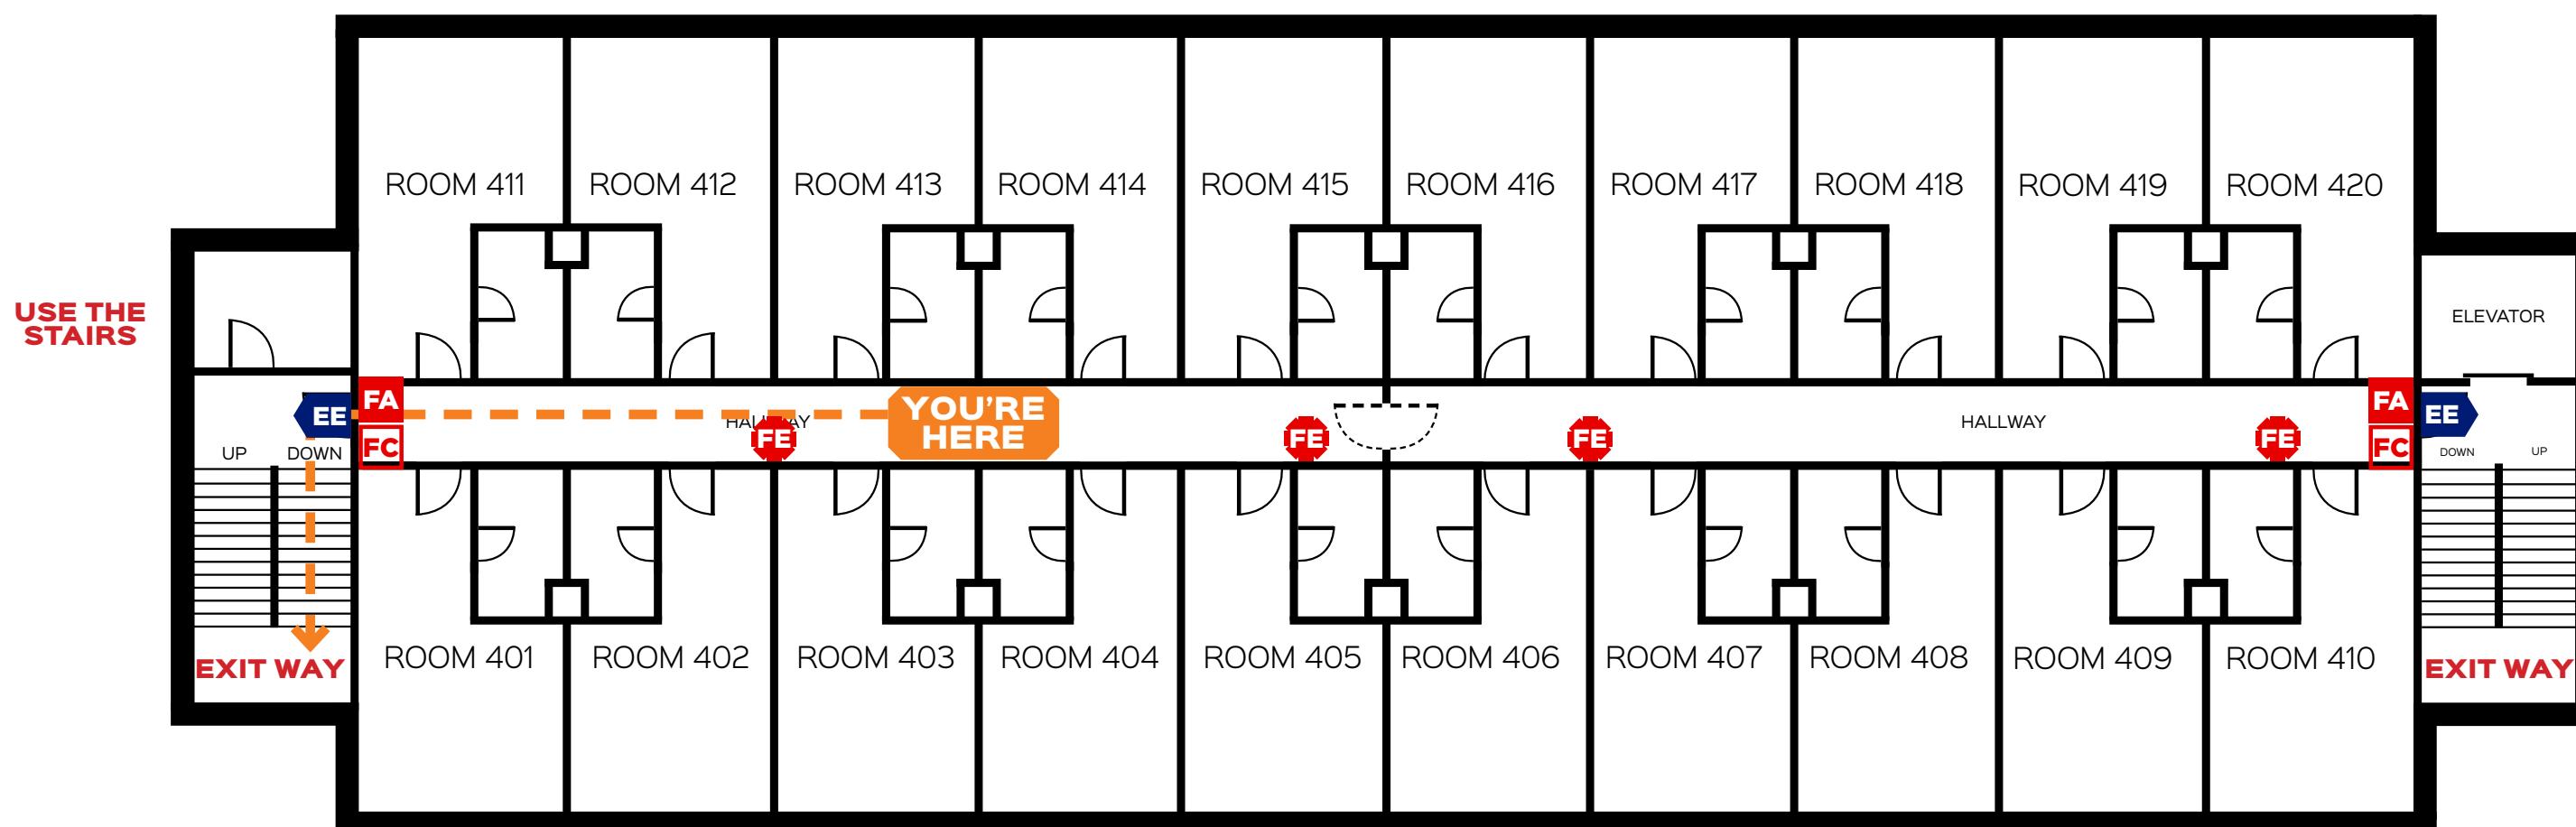

## LEGEND



# **FA FIRE ALARM**



# **FH FIRE HYDRANT**




# **YOU'RE HERE** CURRENT LOCATION



## — DIRECTIONAL EXIT SIGNS



**FS FDAS PANEL**

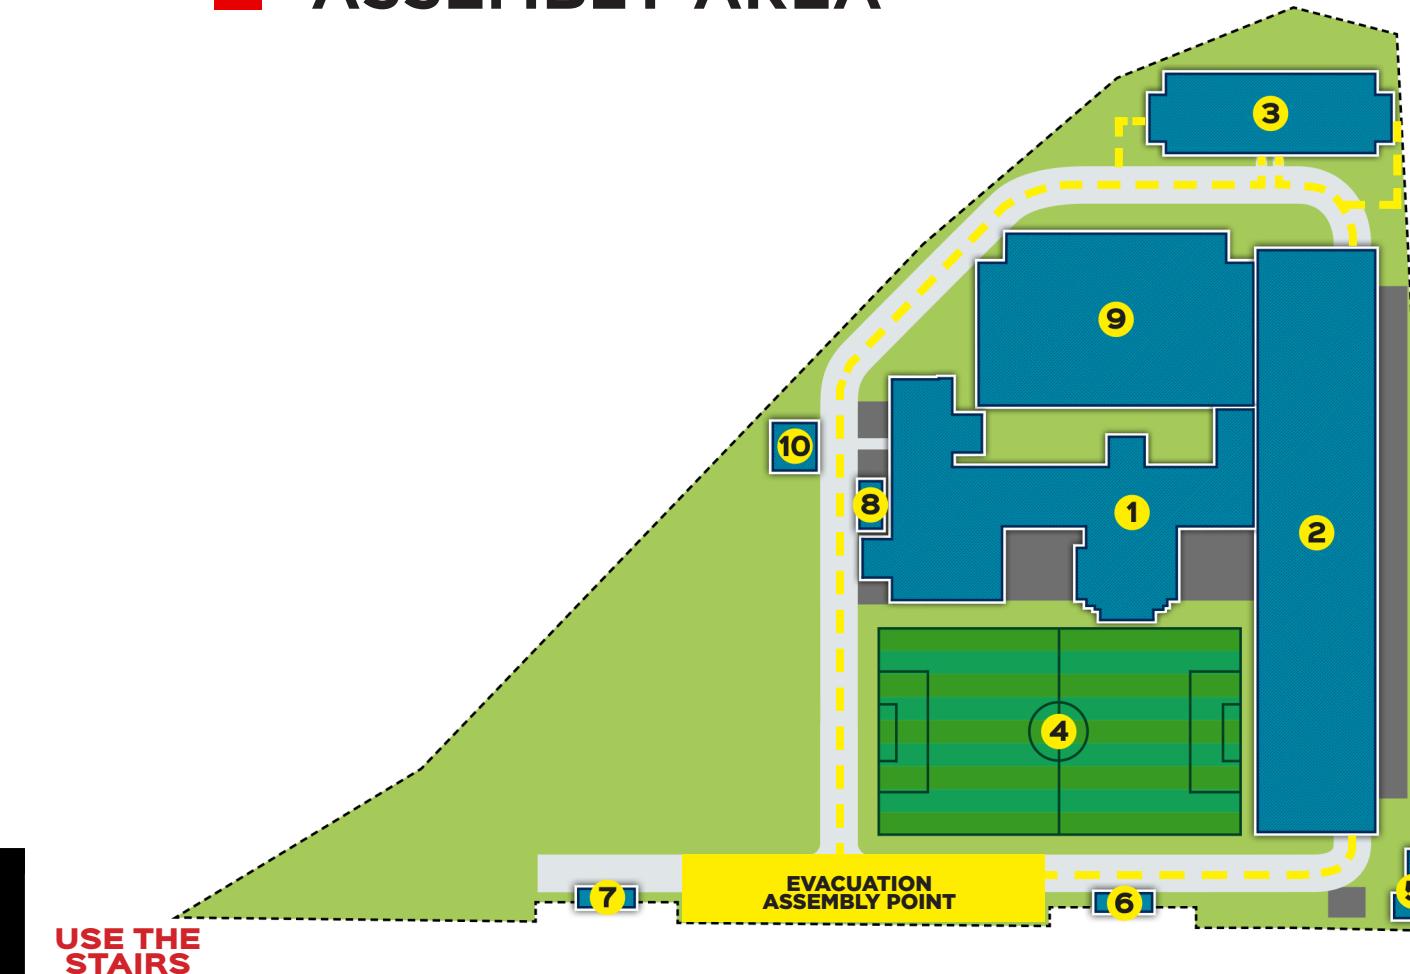

## IN CASE OF EMERGENCY

- **Remain calm, do not panic.**
  - **Remove all persons from danger.**
  - **In case of emergency, do not use the elevator. Leave the building using the nearest fire exit route.**
  - **WALK, DO NOT RUN.**
  - **Activate fire alarm.**

# ASSEMBLY AREA REMINDERS

- Account for persons missing from the building.
  - Report any missing persons to the emergency response team.
  - DO NOT re-enter the building until the “ALL CLEAR” is given by the responding emergency service.


# EMERGENCY NUMBERS

**CLINIC** (63) 998 961 1923  
**PFMO/ SECURITY** (63) 998 988 1908  
**FIRE** (63) 945 490 4131  
**POLICE** (049) 545 1698  
**CDRRMO & POSO** (63) 917 148 9813  
**AMBULANCE** (049) 545 1740

# EVACUATION MAP

FOURTH FLOOR  
DORMITEL

## HALLWAY IN BETWEEN ROOM 407 AND ROOM 408

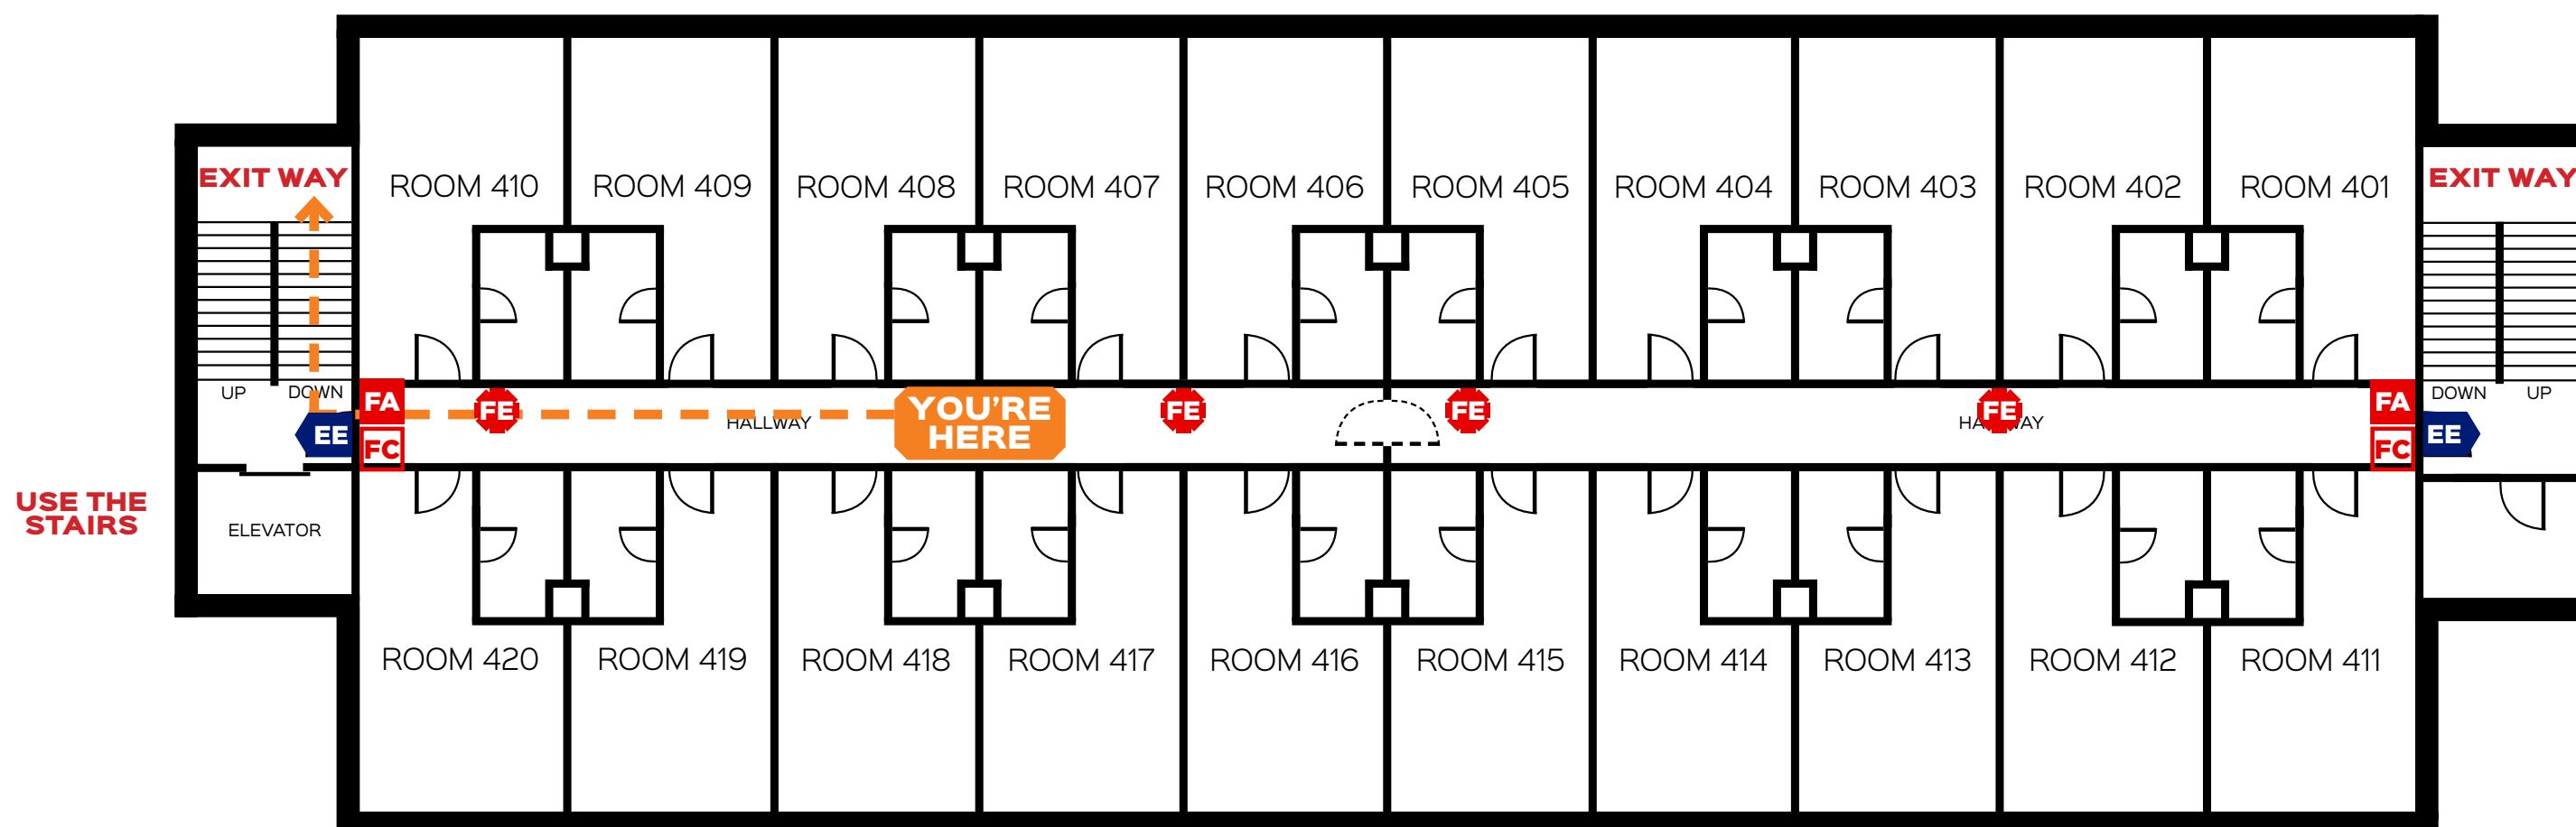

### LEGEND



**FE** FIRE EXTINGUISHER



**FA** FIRE ALARM



EMERGENCY EXIT



**FC** FIRE HOSE CABINET

**FH** FIRE HYDRANT



**UP** **DOWN** STAIRS



**FA** FIRST AID KIT

CURRENT LOCATION




DIRECTIONAL EXIT SIGNS



**FS** FDAS PANEL

### ■ ASSEMBLY AREA

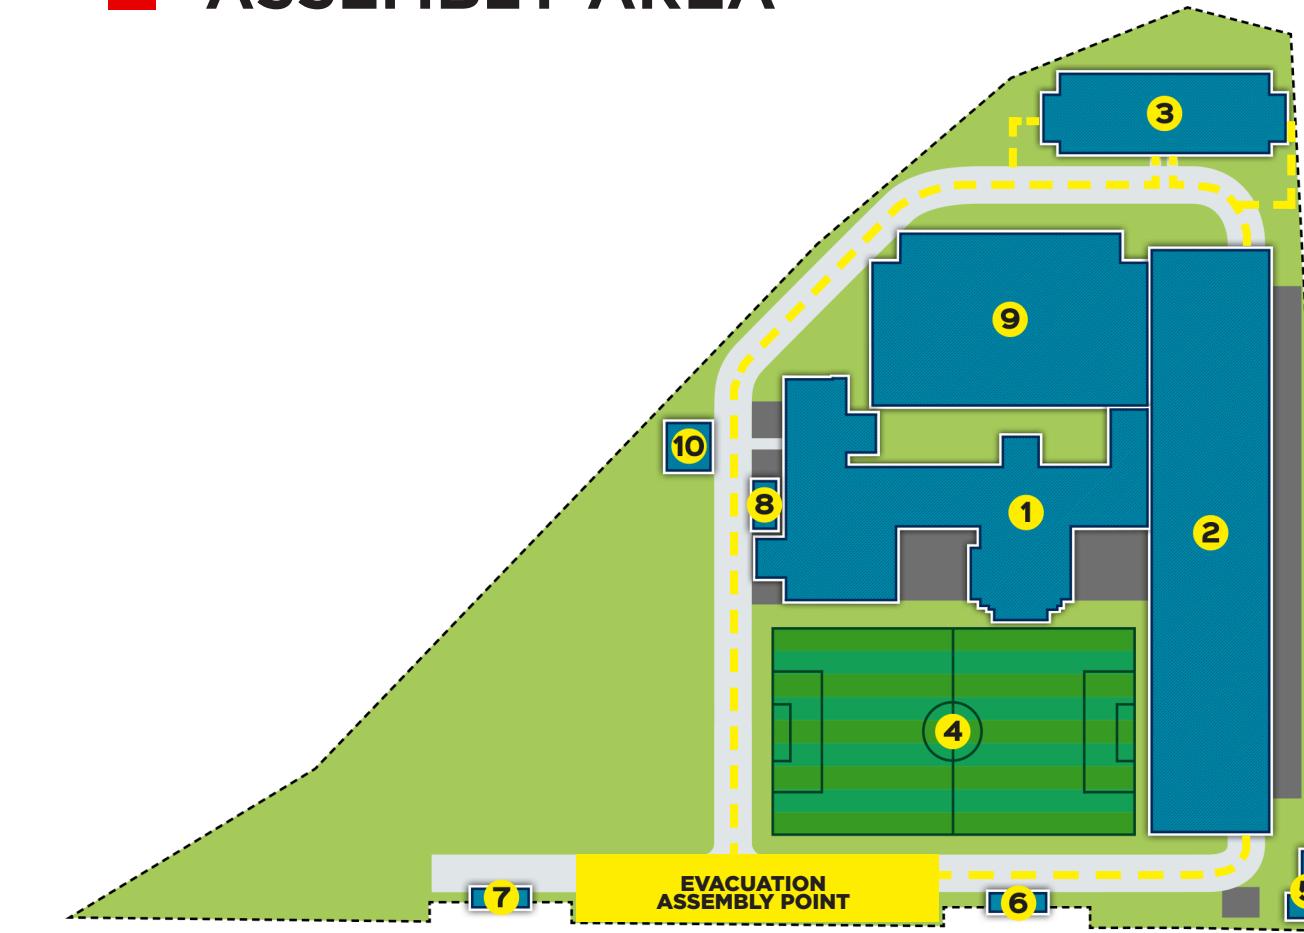

- **IN CASE OF EMERGENCY**
  - Remain calm, do not panic.
  - Remove all persons from danger.
  - In case of emergency, do not use the elevator. Leave the building using the nearest fire exit route.
  - WALK, DO NOT RUN.
  - Activate fire alarm.
- **ASSEMBLY AREA REMINDERS**
  - Account for persons missing from the building.
  - Report any missing persons to the emergency response team.
  - DO NOT re-enter the building until the "ALL CLEAR" is given by the responding emergency service.
- **EMERGENCY NUMBERS**


CLINIC	(63) 998 961 1923
PFMO/ SECURITY	(63) 998 988 1908
FIRE	(63) 945 490 4131
POLICE	(049) 545 1698
CDRRMO & POSO	(63) 917 148 9813
AMBULANCE	(049) 545 1740

**FIFTH FLOOR**


# EVACUATION MAP

FIFTH FLOOR  
DORMITEL

## ROOF DECK ALFRESCO LOUNGE RIGHT WING

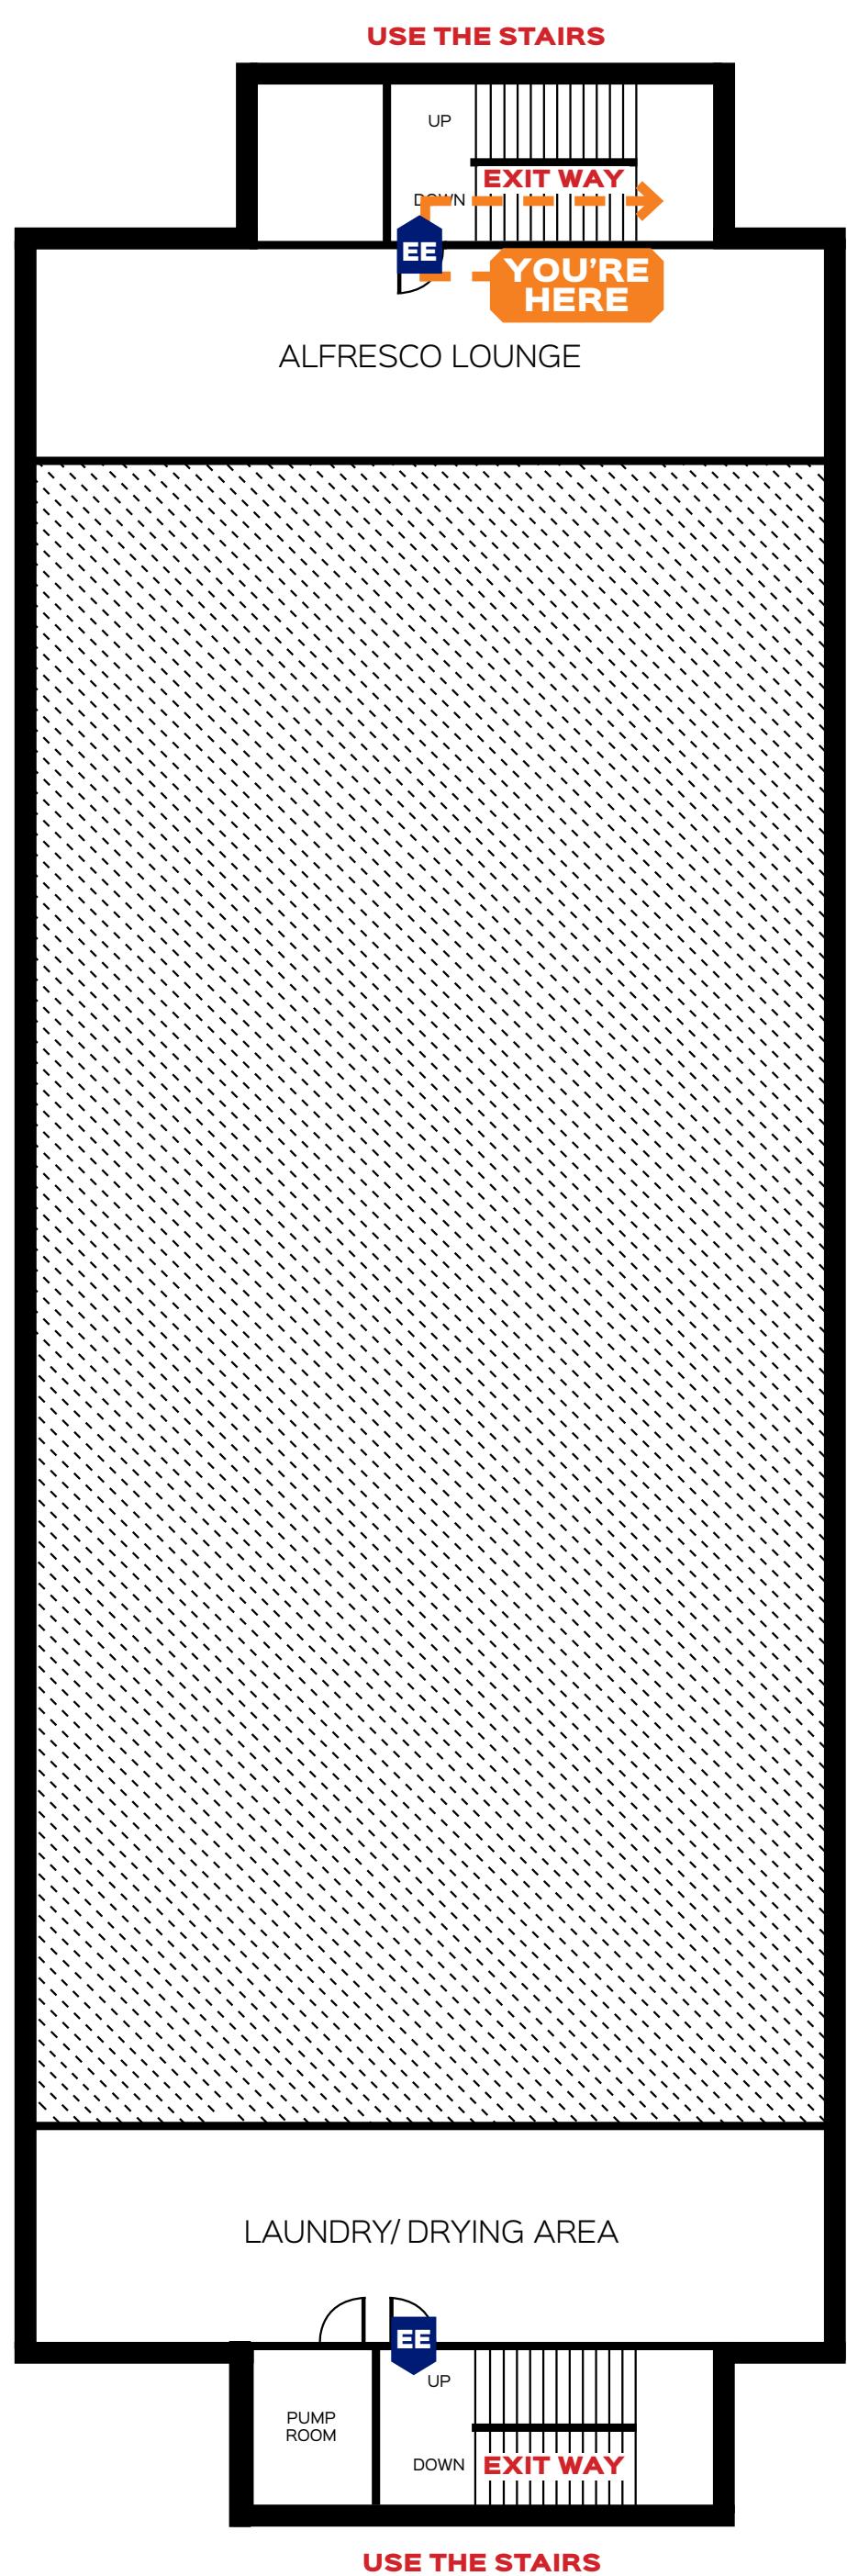

### ■ ASSEMBLY AREA

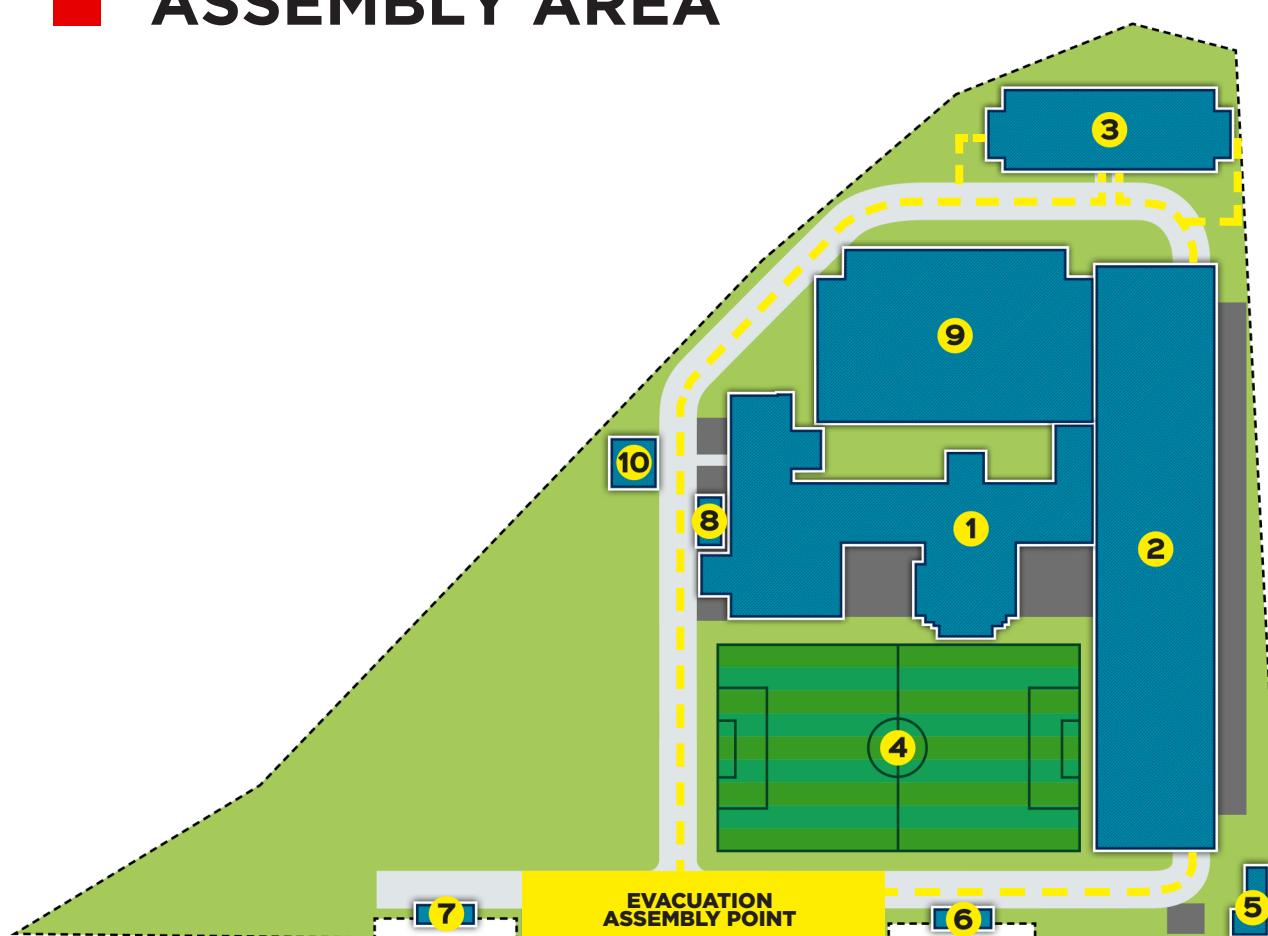

### ■ IN CASE OF EMERGENCY

- Remain calm, do not panic.
- Remove all persons from danger.
- In case of emergency, do not use the elevator. Leave the building using the nearest fire exit route.
- WALK, DO NOT RUN.
- Activate fire alarm.


### ■ ASSEMBLY AREA REMINDERS

- Account for persons missing from the building.
- Report any missing persons to the emergency response team.
- DO NOT re-enter the building until the "ALL CLEAR" is given by the responding emergency service.

### ■ EMERGENCY NUMBERS

CLINIC	(63) 998 961 1923
PFMO/ SECURITY	(63) 998 988 1908
FIRE	(63) 945 490 4131
POLICE	(049) 545 1698
CDRRMO & POSO	(63) 917 148 9813
AMBULANCE	(049) 545 1740


### ■ LEGEND

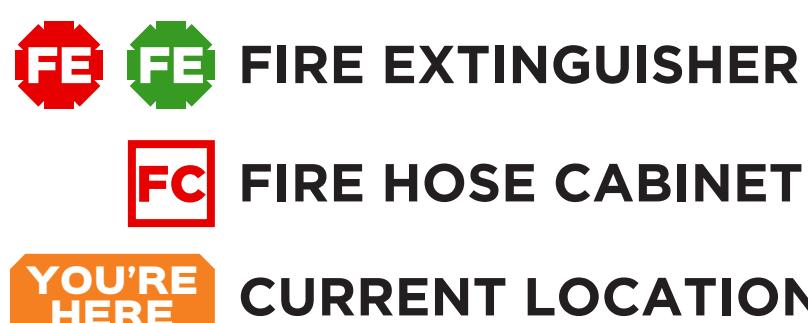


# EVACUATION MAP

FIFTH FLOOR  
DORMITEL

## ROOF DECK LAUNDRY/ DRYING AREA LEFT WING

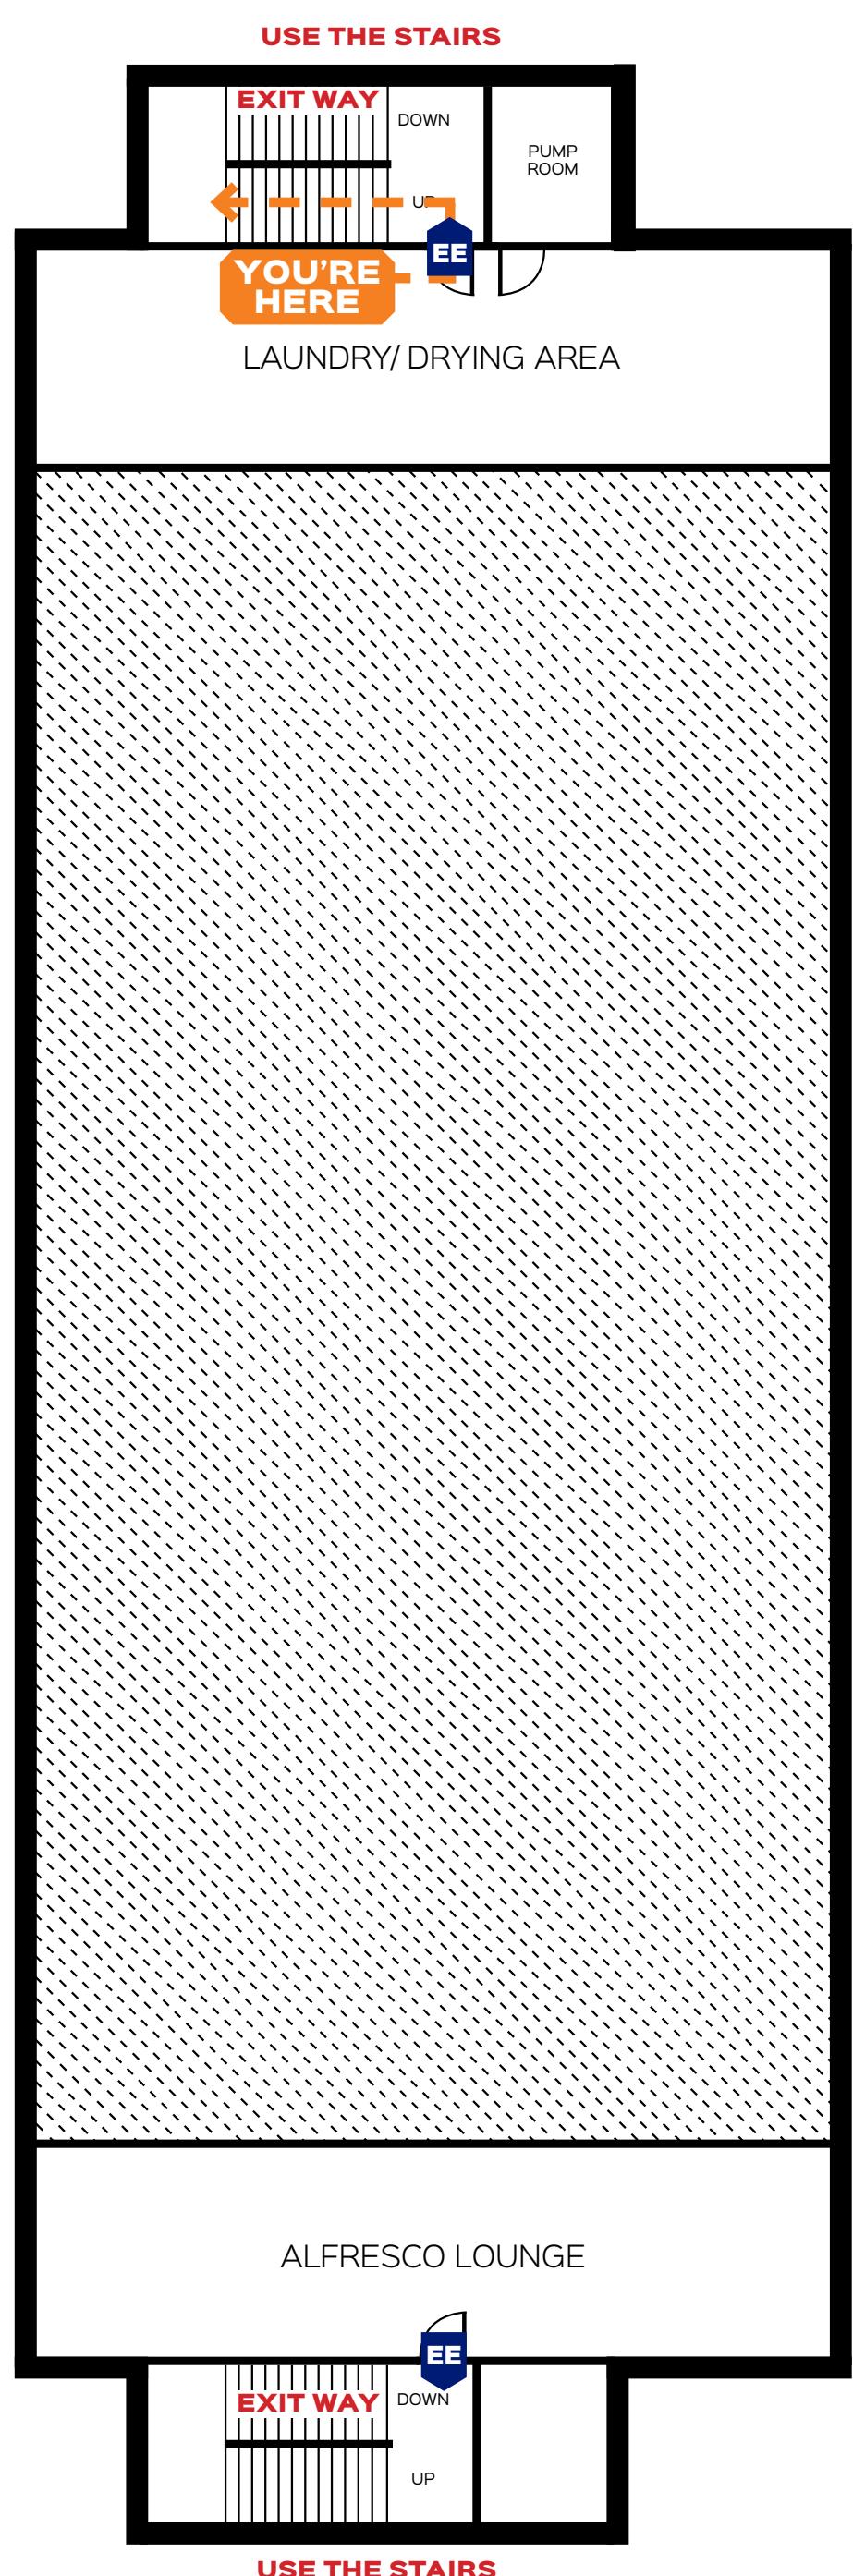

### ■ ASSEMBLY AREA

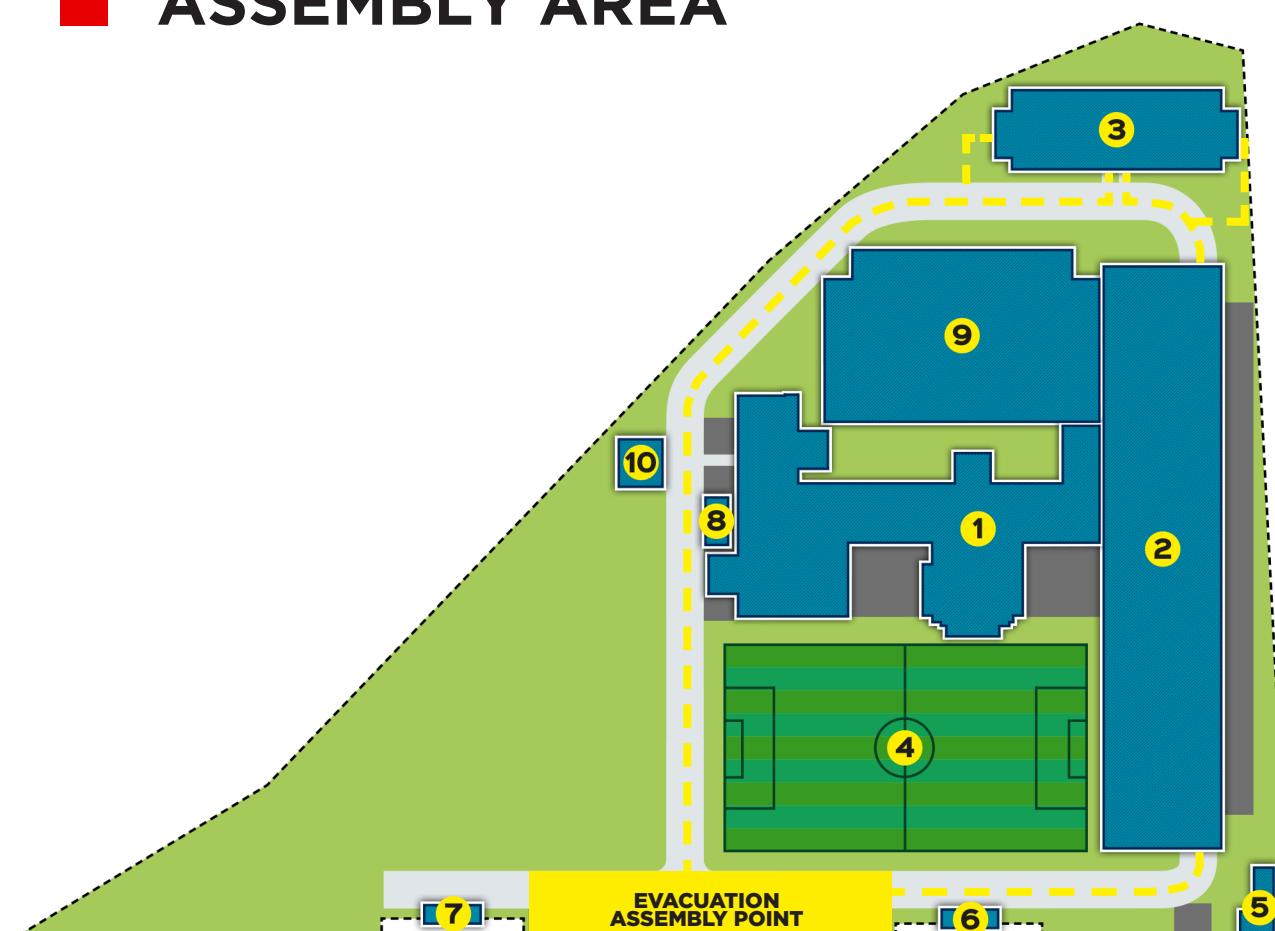

### ■ IN CASE OF EMERGENCY

- Remain calm, do not panic.
- Remove all persons from danger.
- In case of emergency, do not use the elevator. Leave the building using the nearest fire exit route.
- WALK, DO NOT RUN.
- Activate fire alarm.

### ■ ASSEMBLY AREA REMINDERS

- Account for persons missing from the building.
- Report any missing persons to the emergency response team.
- DO NOT re-enter the building until the "ALL CLEAR" is given by the responding emergency service.

### ■ EMERGENCY NUMBERS

CLINIC	(63) 998 961 1923
PFMO/ SECURITY	(63) 998 988 1908
FIRE	(63) 945 490 4131
POLICE	(049) 545 1698
CDRRMO & POSO	(63) 917 148 9813
AMBULANCE	(049) 545 1740

### ■ LEGEND



FIRE EXTINGUISHER



FIRE ALARM



EMERGENCY EXIT



FIRE HOSE CABINET



FIRE HYDRANT



STAIRS



FIRST AID KIT



CURRENT LOCATION



DIRECTIONAL EXIT SIGNS



FDAS PANEL